







CAMPBELL RESIDENCE

Lot 1213 in Troubadour
College Grove, Tennessee



07.23.26

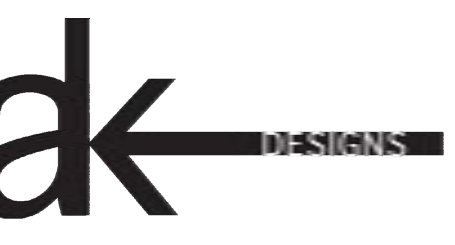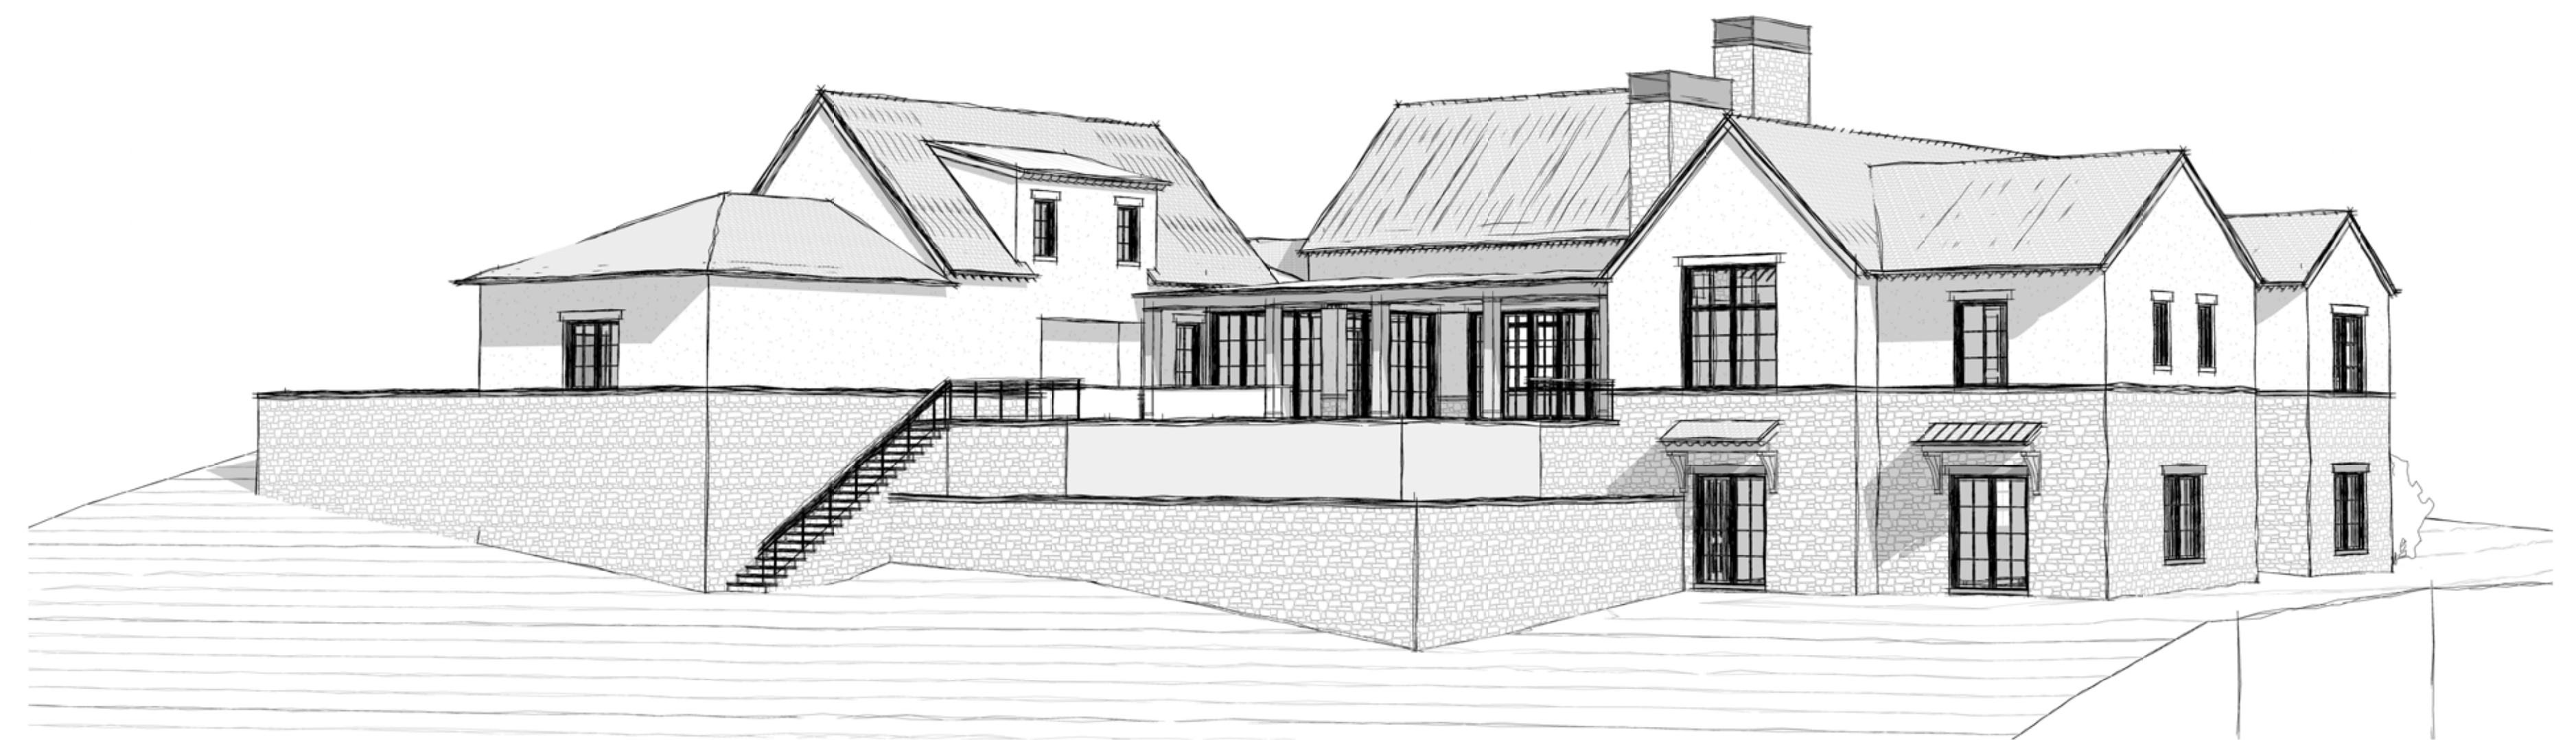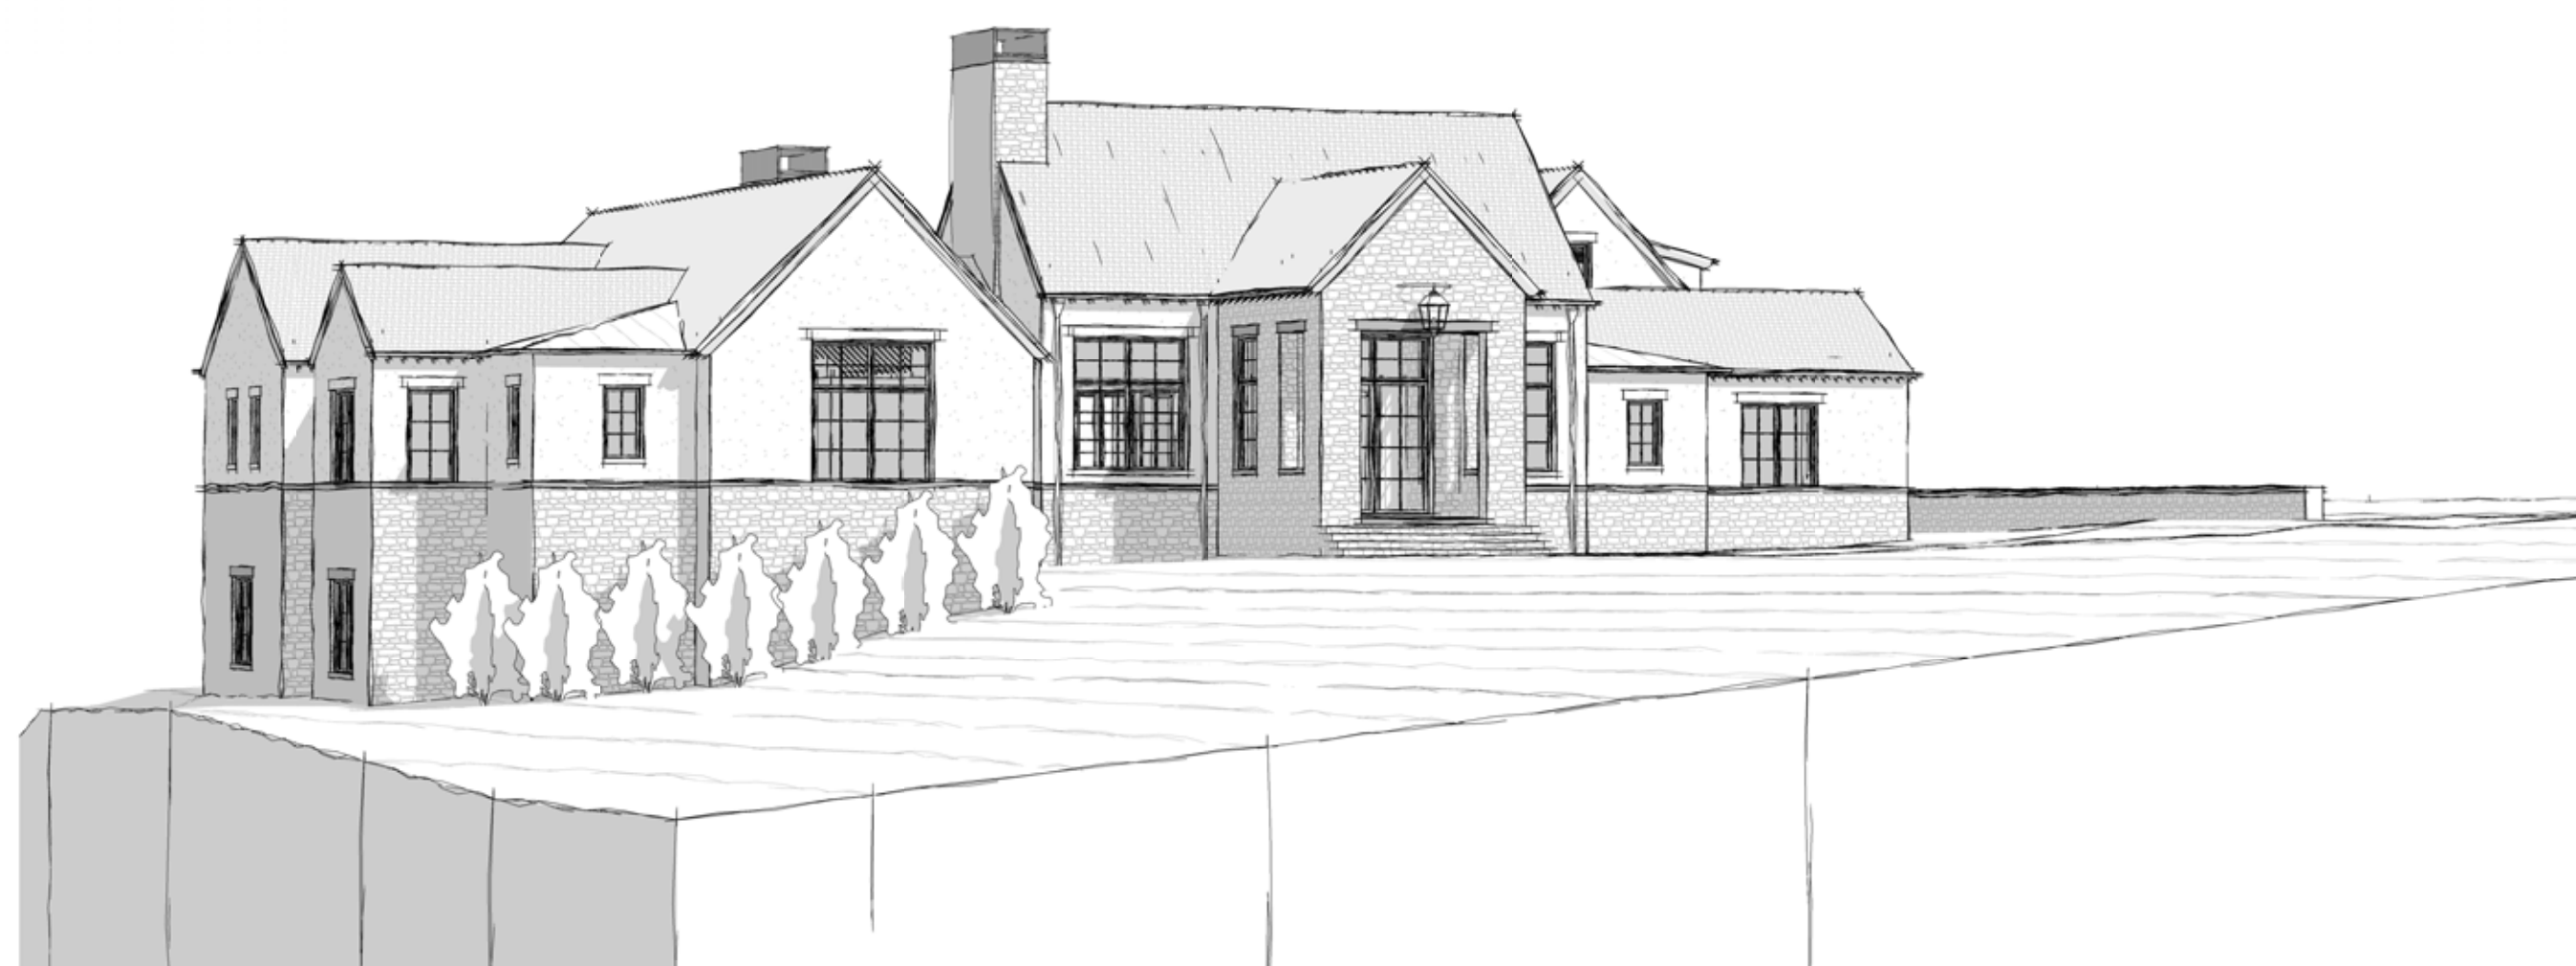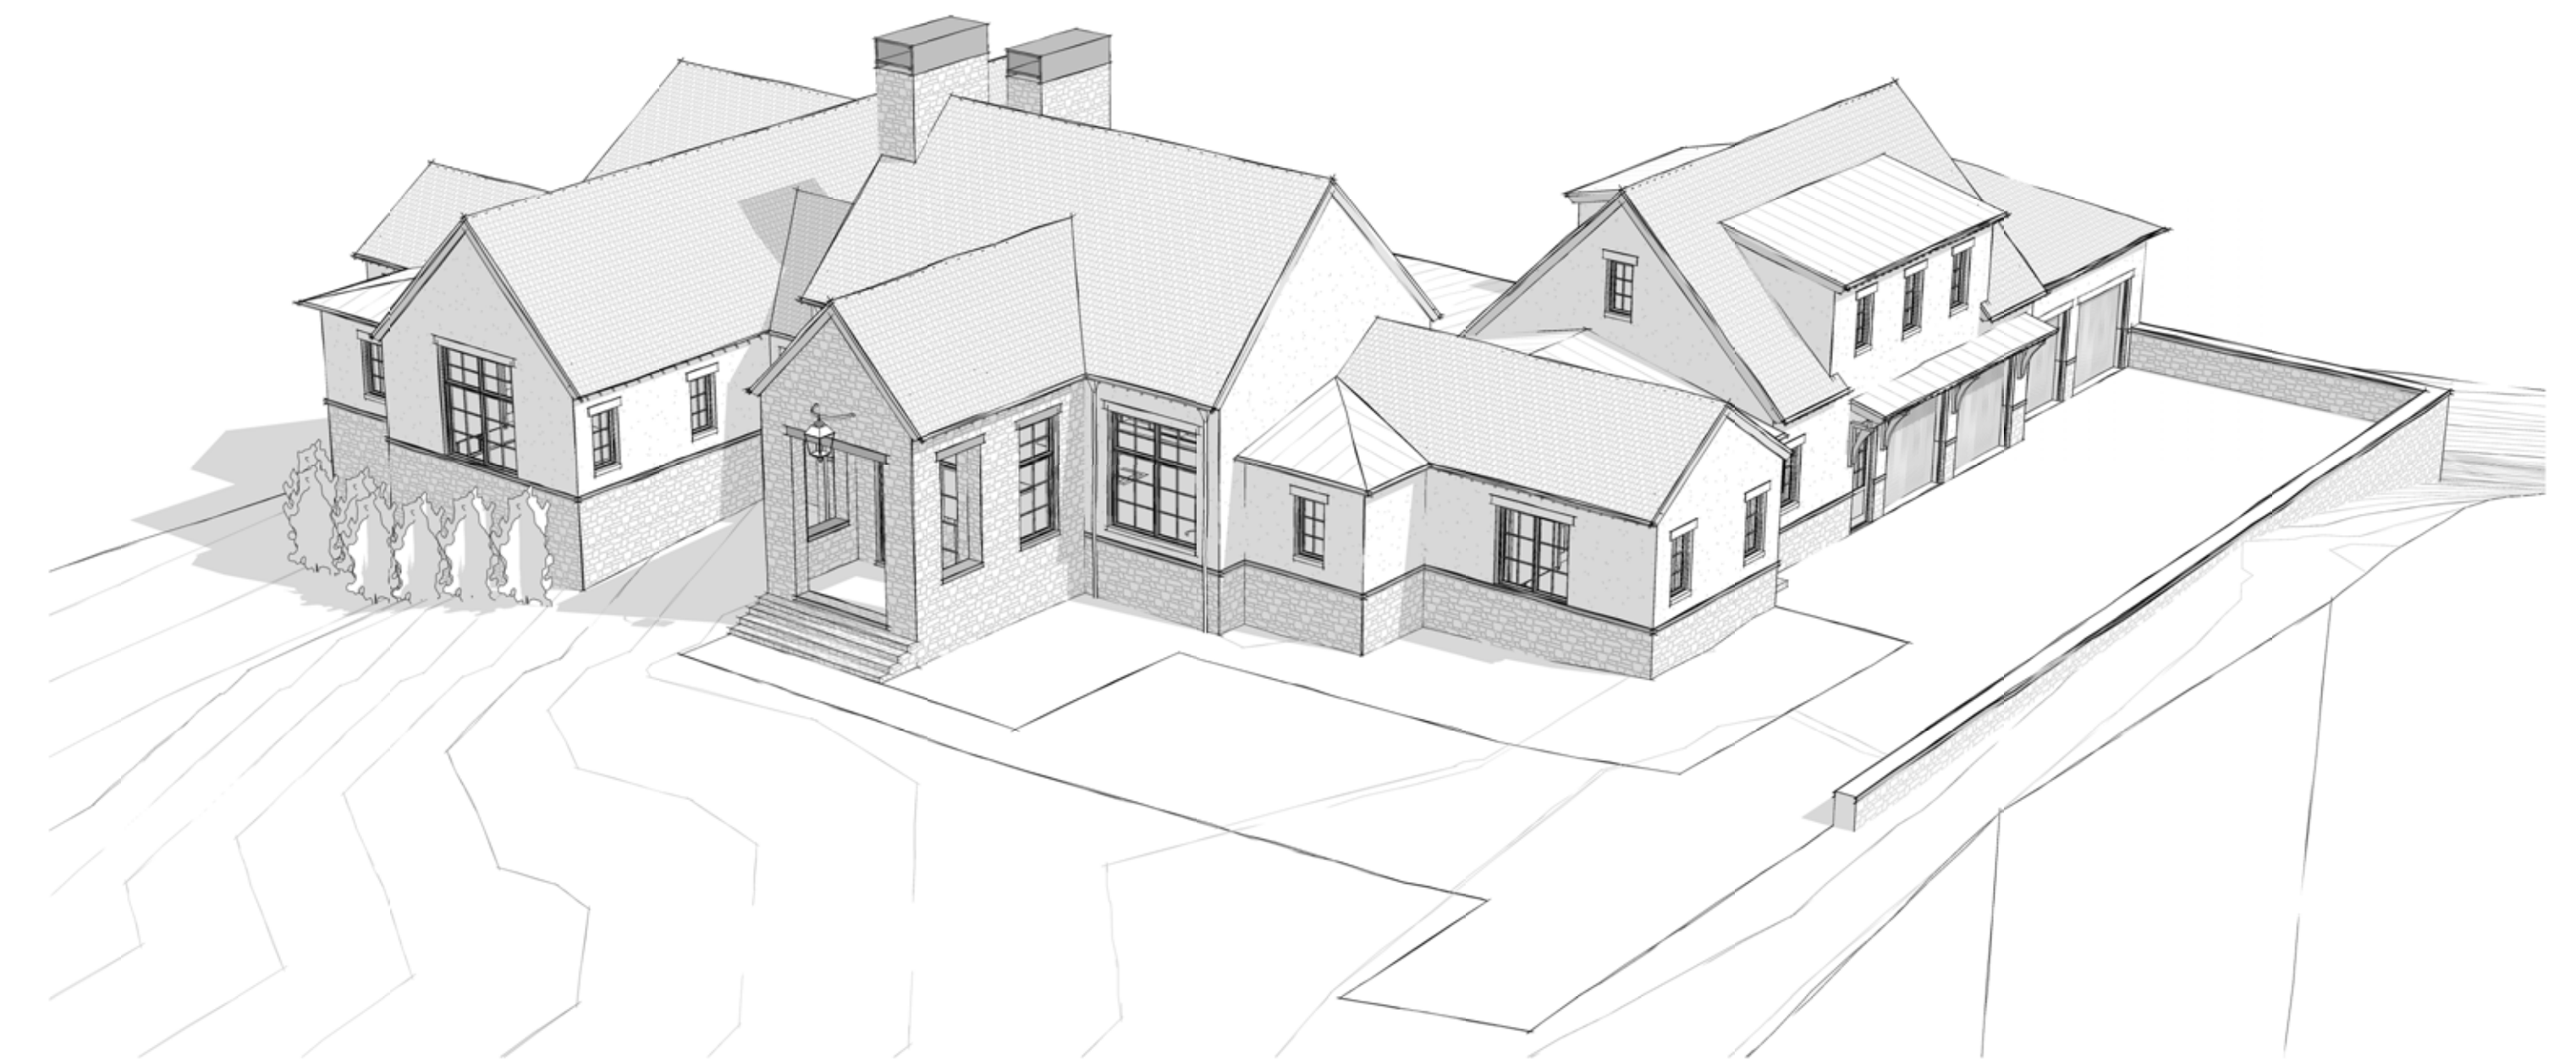

ak designs
205 Powell Place, Suite 119
Brentwood, TN 37027

DESIGN
DEVELOPMENT
not for construction

This document is an instrument of service and shall remain the property of ak designs. No portion of this document may be reproduced or transmitted in any form or by any means, including electronic, mechanical, photocopying, recording, or by any information storage and retrieval system, without the prior written permission of ak designs.

Copyright © 2026
ak designs

CAMPBELL RESIDENCE

Lot 1213 in Troubadour
College Grove, Tennessee


Perspectives

Revision Date:

1.	
2.	
3.	
4.	
5.	
6.	

Project Number: A21018
Date: 07.23.26
Scale:

Sheet
G001

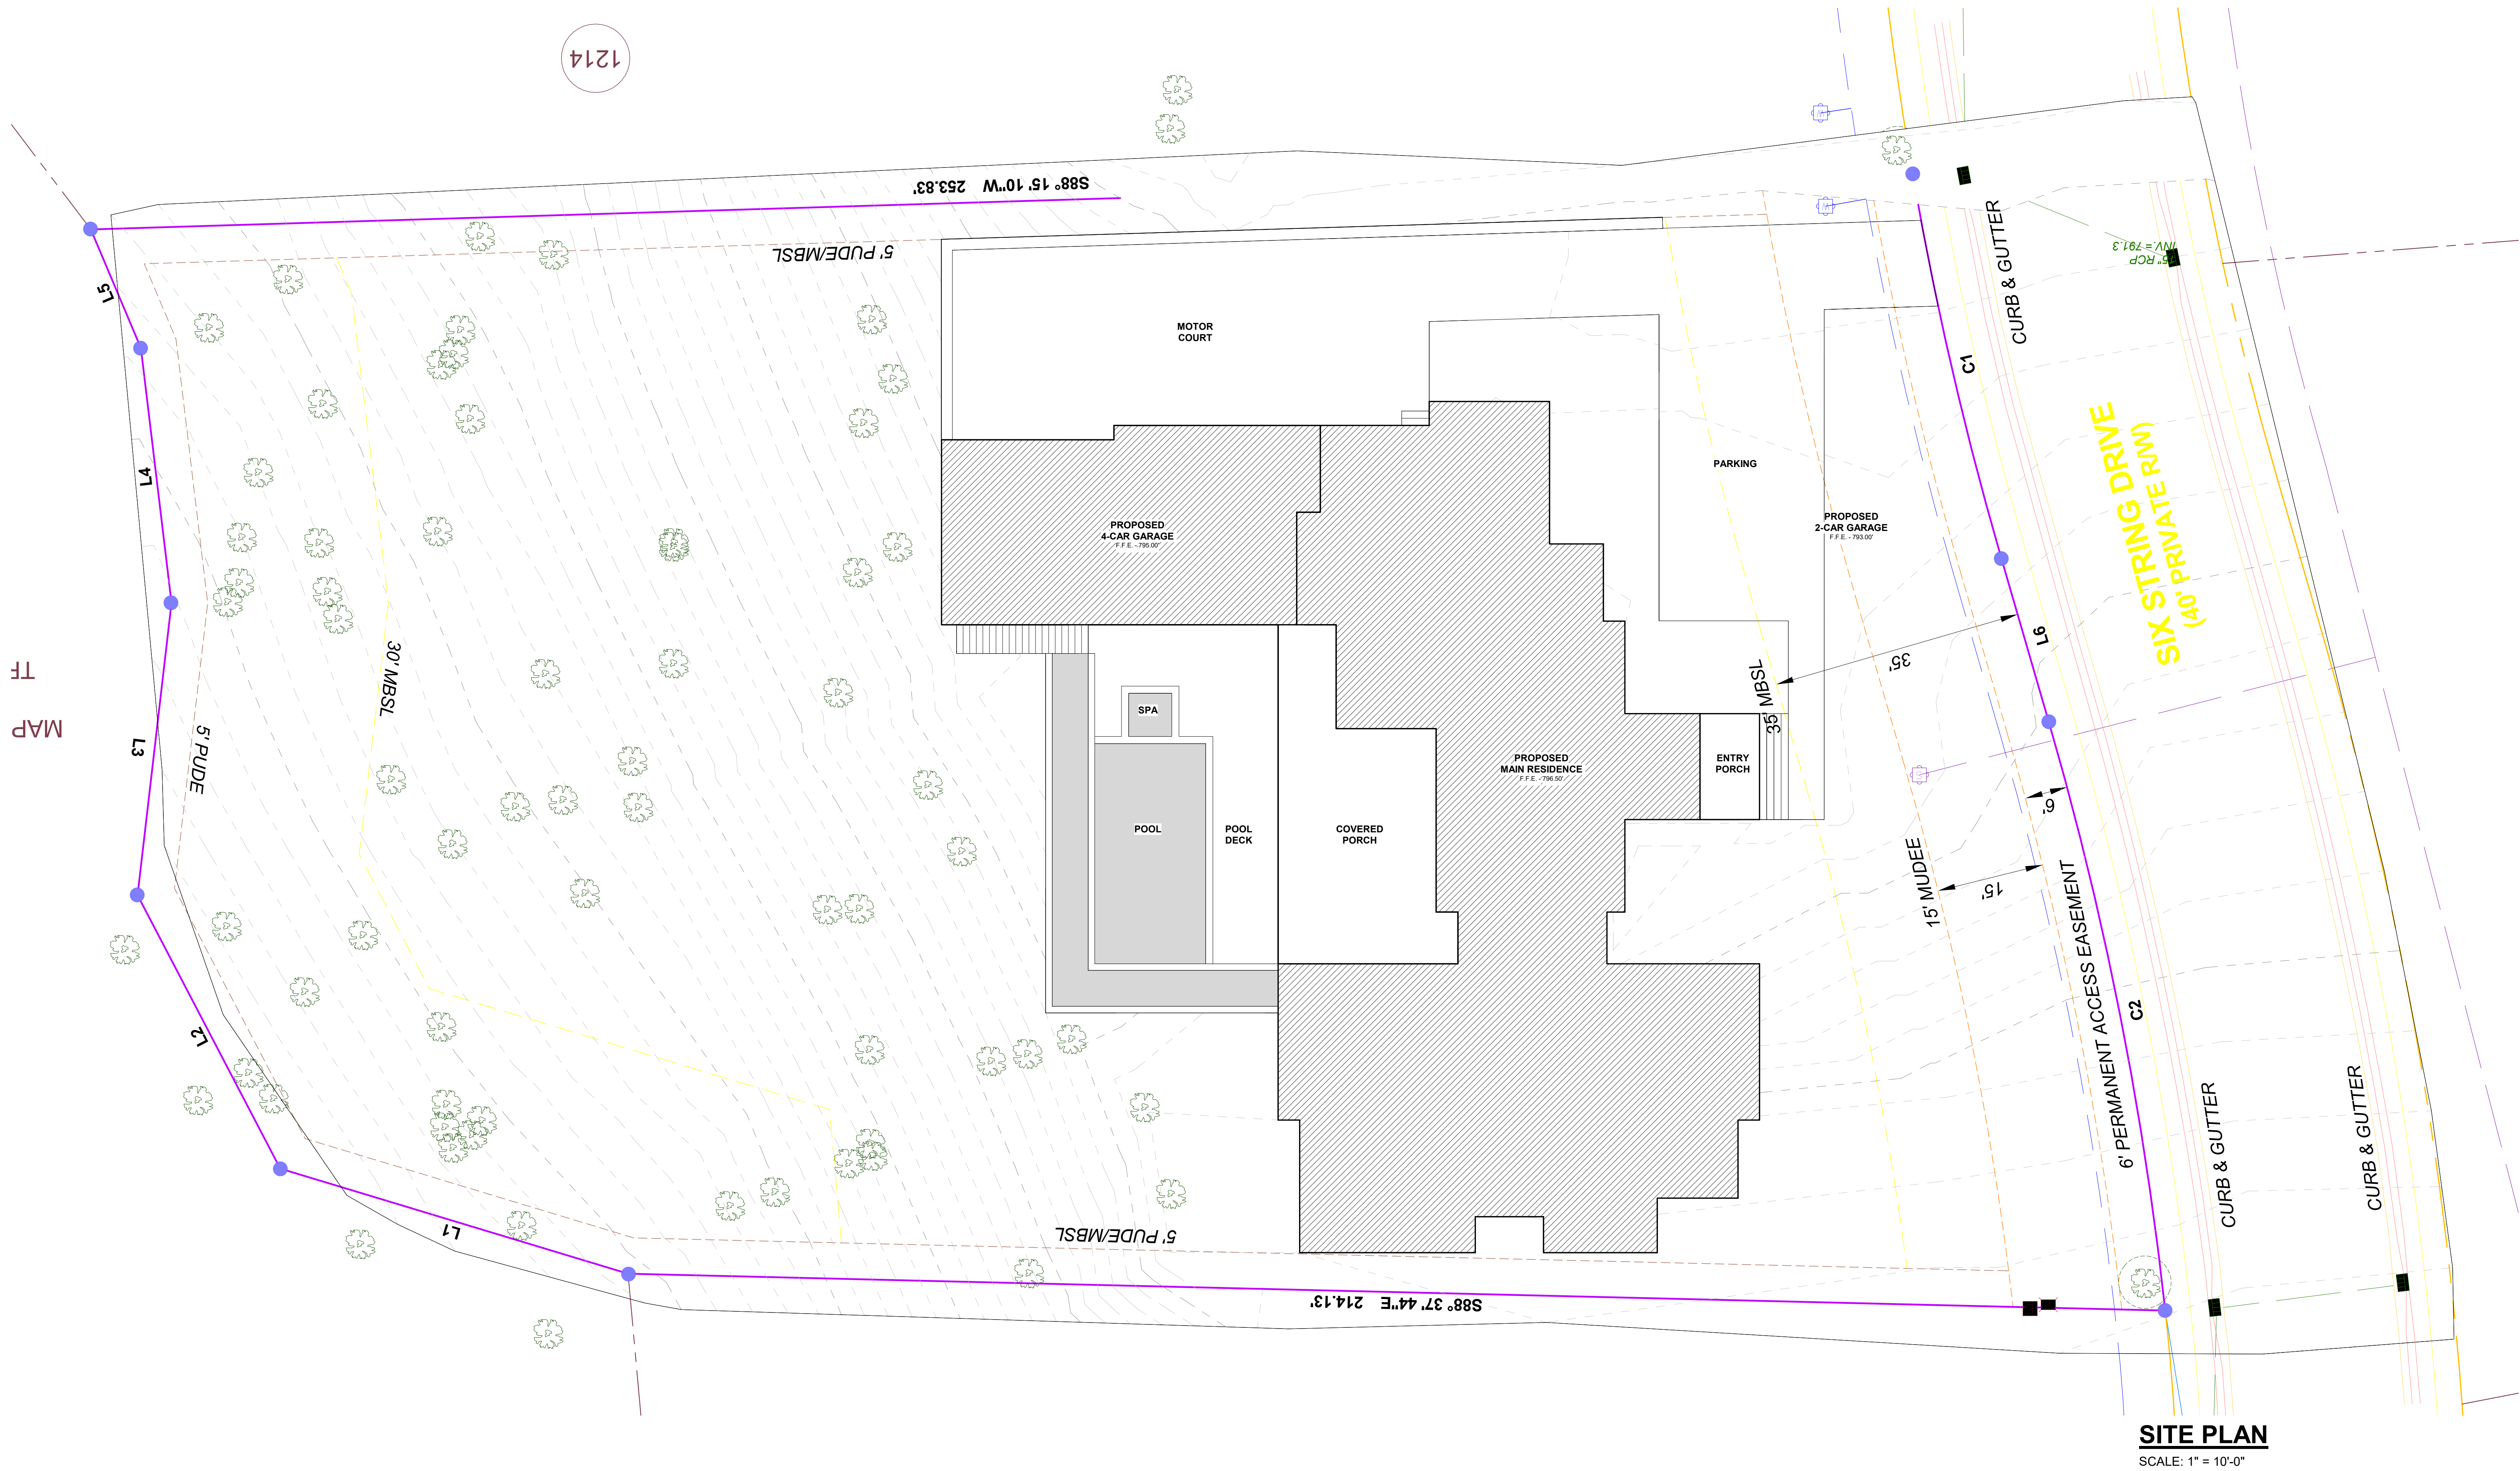

SITE PLAN
SCALE: 1" = 10'-0"

SITE PLAN NOTES

GENERAL LOT INFORMATION IS DEEMED RELIABLE AND CURRENT, HOWEVER IT IS THE BUILDER'S RESPONSIBILITY TO ENSURE COMPLIANCE WITH BUILDING SETBACKS, EASEMENTS AND ALL APPLICABLE BUILDING CODES, AND TO VERIFY PROPERTY LINE LOCATION AND BOUNDARIES. NOTIFY DESIGNER OF ANY DISCREPANCIES PRIOR TO CONSTRUCTION.

DIMENSIONS: ALL DIMENSION STRINGS ARE SHOWN TO OUTSIDE FACE OF 12" BLOCK (ALLOW FOR 2" (17") BRICK OVERAGE WITHIN SETBACKS) AND ARE PERPENDICULAR TO PROPERTY LINES.

GRADING: BUILDER TO ENSURE POSITIVE DRAINAGE AWAY FROM STRUCTURE. IT IS THE BEST INTEREST OF THE BUILDER TO CONSULT A LANDSCAPE ARCHITECT OR CIVIL ENGINEER FOR DETAILED GRADING AND DRAINAGE PLANS.

PAVING: STREET LOADED DRIVES SHALL HAVE CURB CUTS OF 12". ALLEY LOADED DRIVES SHALL BE MINIMUM 24" WIDER THAN INDICATED GARAGE DOOR. LEAD WALKS SHALL MATCH THE WIDTH OF THE BOTTOM PORCH STEP AND TAPER TO NO LESS THAN 3" AT SIDEWALK.

UTILITIES: VERIFY UTILITIES DO NOT IMPACT DRIVE OR WALKWAY PAVING PRIOR TO CONSTRUCTION. NOTIFY DESIGNER OF ANY DISCREPANCIES PRIOR TO CONSTRUCTION.

CAMPBELL RESIDENCE


Lot 1213 in Troubadour
College Grove, Tennessee

Site Plan

Revision Date:

1.	
2.	
3.	
4.	
5.	
6.	

Project Number: A21018
Date: 07/23/26
Scale: As indicated

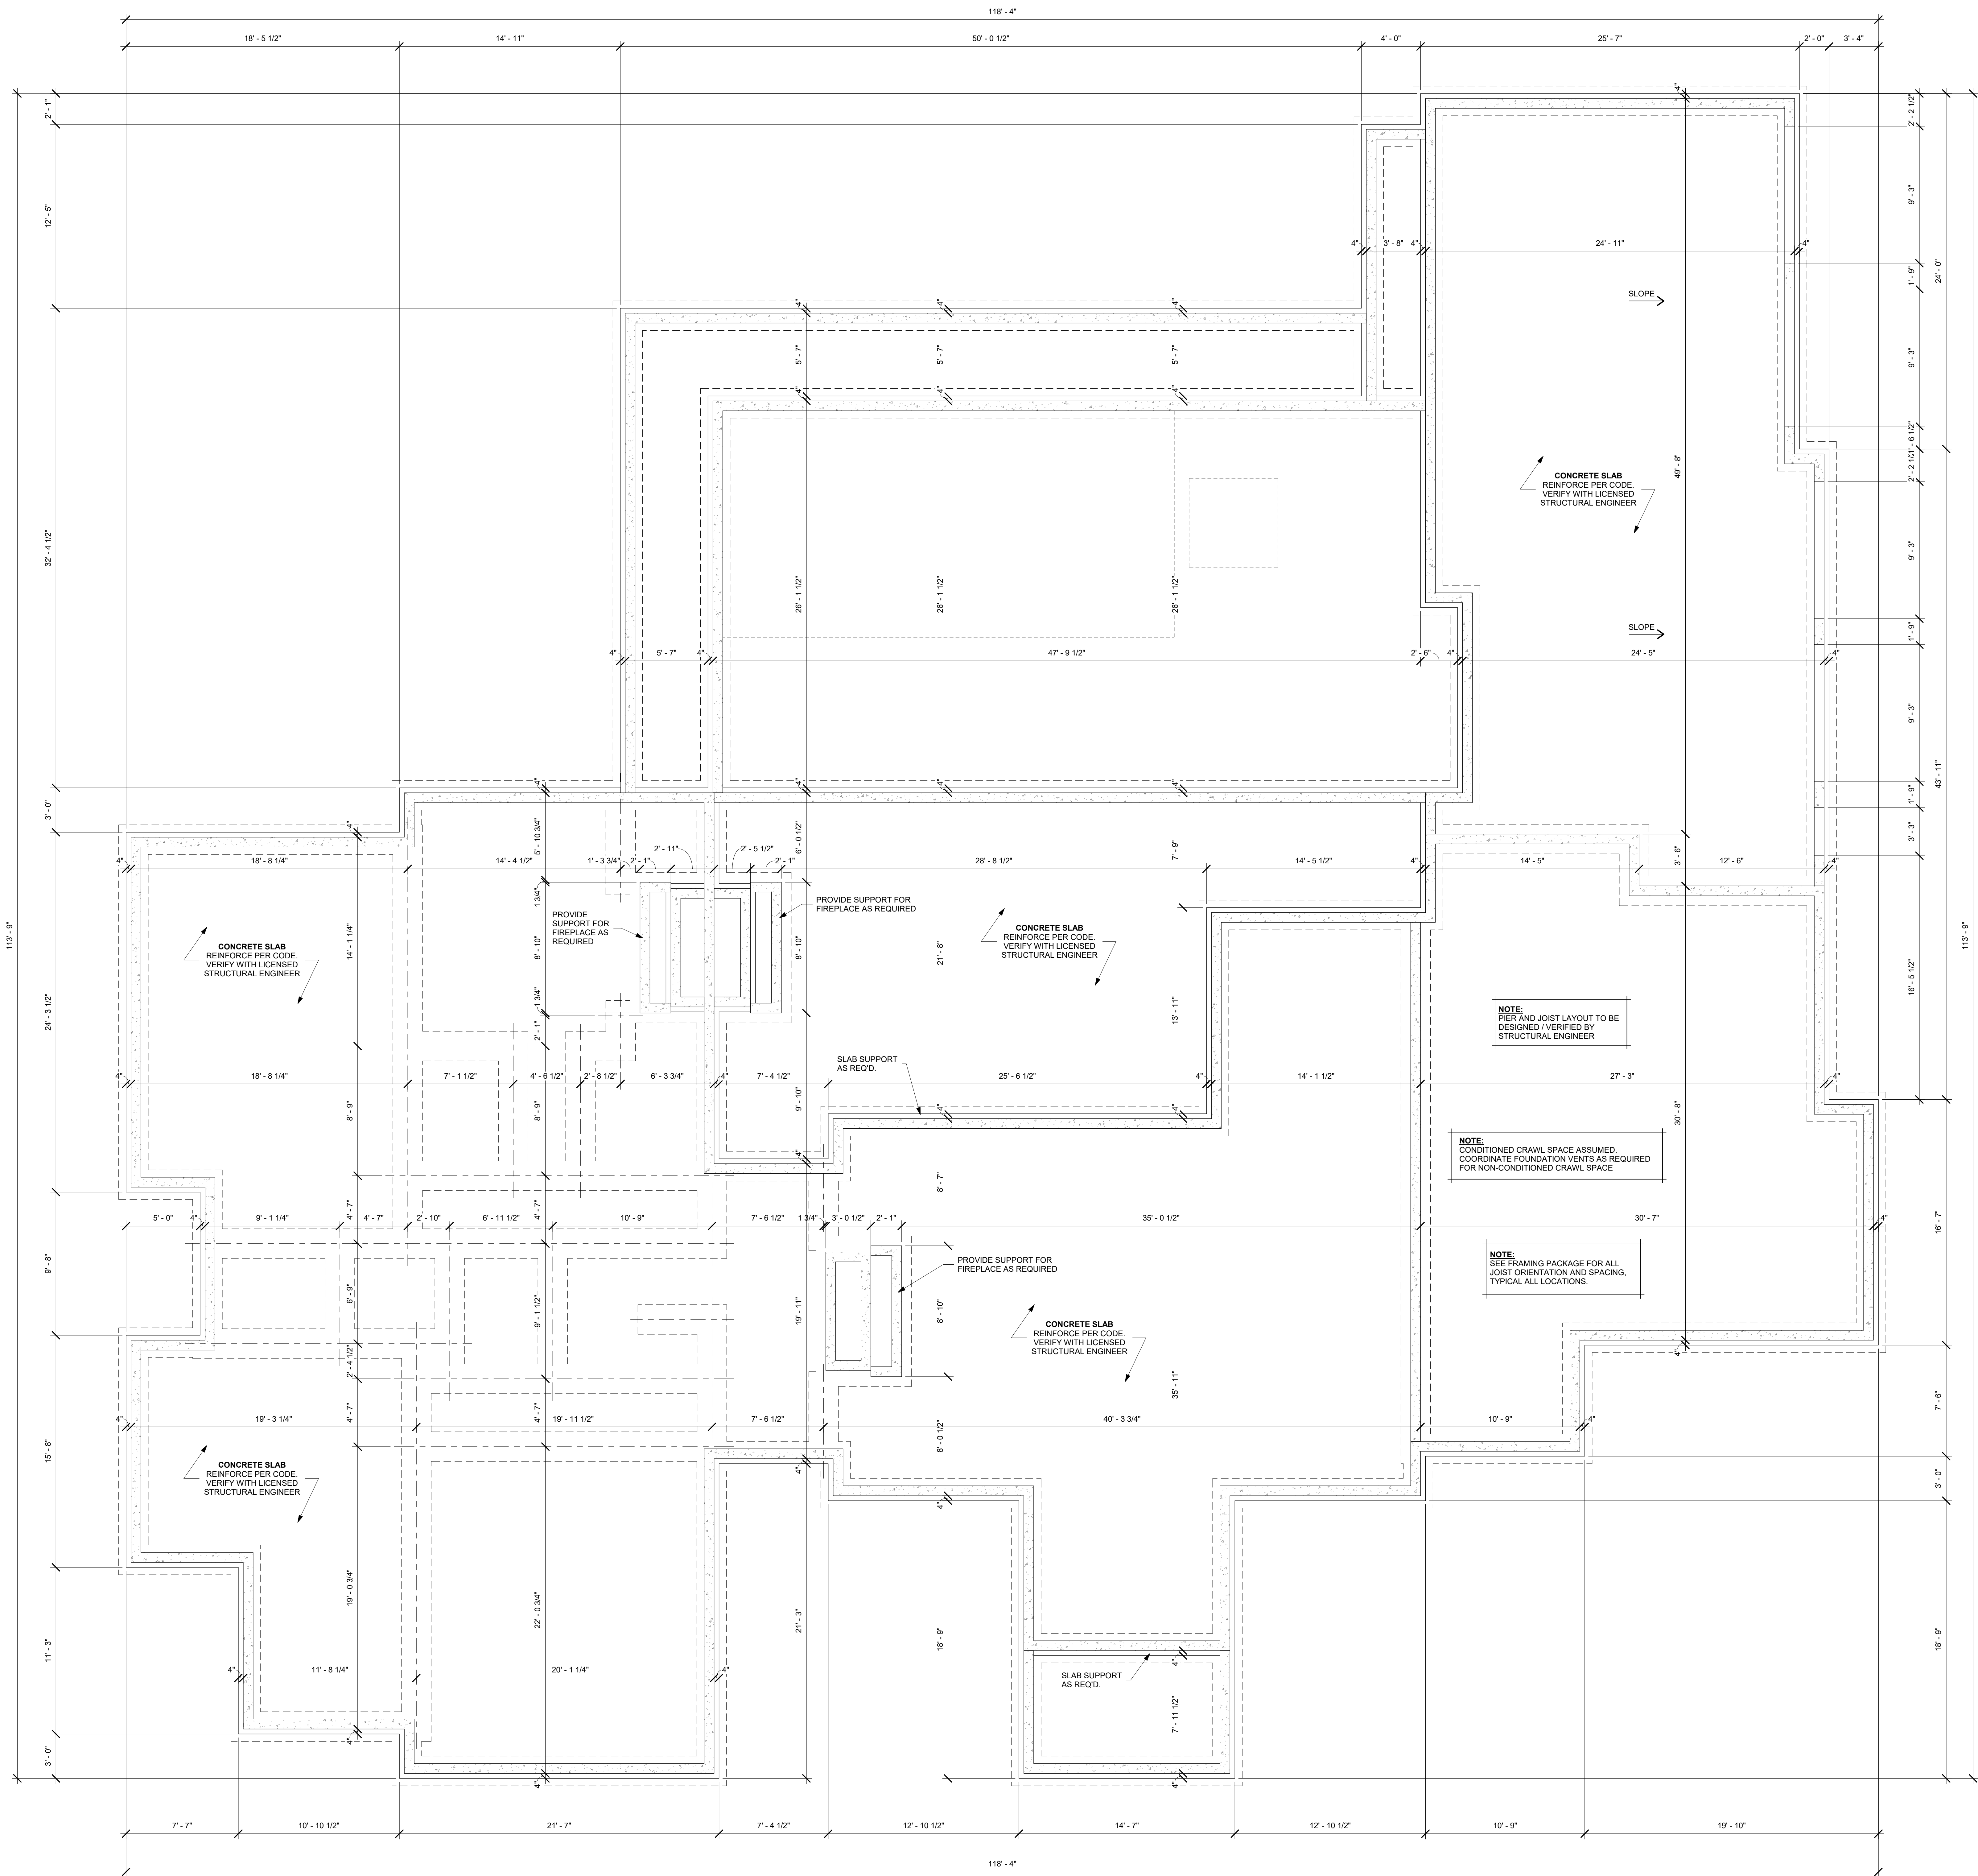

FOUNDATION PLAN
SCALE: 1/4" = 1'-0"

- GENERAL FOUNDATION NOTES**
- BUILDER TO SIZE ALL BEAMS AND FRAMING MEMBERS OF UPPER LEVEL(S) PRIOR TO CONSTRUCTION.
 - PERIMETER DIMENSIONS ARE TO OUTSIDE FACE OF 12" BLOCK. INTERNAL DIMENSIONS ARE TO OUTSIDE FACE OF 6" BLOCK AND CENTER LINES OF BEAMS / THICKENED SLAB UNLESS NOTED OTHERWISE.
 - BUILDER TO PROVIDE TERMITE TREATMENT UNDER SLABS THAT COMPLY WITH ALL APPLICABLE LOCAL, STATE, AND FEDERAL CODES.
 - ALL INTERIOR FINISH FLOORS SHALL BE FLUSH TO ADJACENT FINISH FLOORS UNLESS NOTED OTHERWISE.
 - ALL STRUCTURAL INFORMATION SHOWN FOR REFERENCE PURPOSES ONLY. BUILDER SHALL HAVE A LICENSED STRUCTURAL ENGINEER REVIEW ACTUAL SITE CONDITIONS PRIOR TO DESIGN OF ALL STRUCTURAL ELEMENTS.
 - IT IS THE BUILDER'S RESPONSIBILITY TO ENSURE THAT ALL WORK AND CONSTRUCTION MEET OR EXCEED APPLICABLE CODES.
 - PROVIDE DOUBLE FLOOR JOISTS UNDER ALL WALLS WHICH RUN PARALLEL TO FLOOR JOISTS.
 - BUILDER TO PROVIDE A "QUIET" FLOOR SYSTEM (GLUE AND SCREW DECKING TO JOISTS.)
 - BUILDER SHALL INSPECT ACTUAL SITE AND EXCAVATED CONDITIONS PRIOR TO STARTING CONSTRUCTION.
 - BUILDER SHALL NOTIFY THE DESIGNER OR LICENSED STRUCTURAL ENGINEER OF ANY NON-TYPICAL CONDITIONS REGARDING SOILS, GROUND WATER, OR ANY OTHER ISSUE WHICH MAY REQUIRE ADDITIONAL OR SPECIAL ENGINEERING.
 - BUILDER SHALL PROVIDE A CONTINUOUS MOISTURE BARRIER BETWEEN MASONRY AND EXPOSED SHEATHING OR FRAMING.

CAMPBELL RESIDENCE


Lot 1213 in Troubadour
College Grove, Tennessee

Foundation Plan

Revision Date:

1.	
2.	
3.	
4.	
5.	
6.	

Project Number: A21018
Date: 07.23.26
Scale: 1/4" = 1'-0"

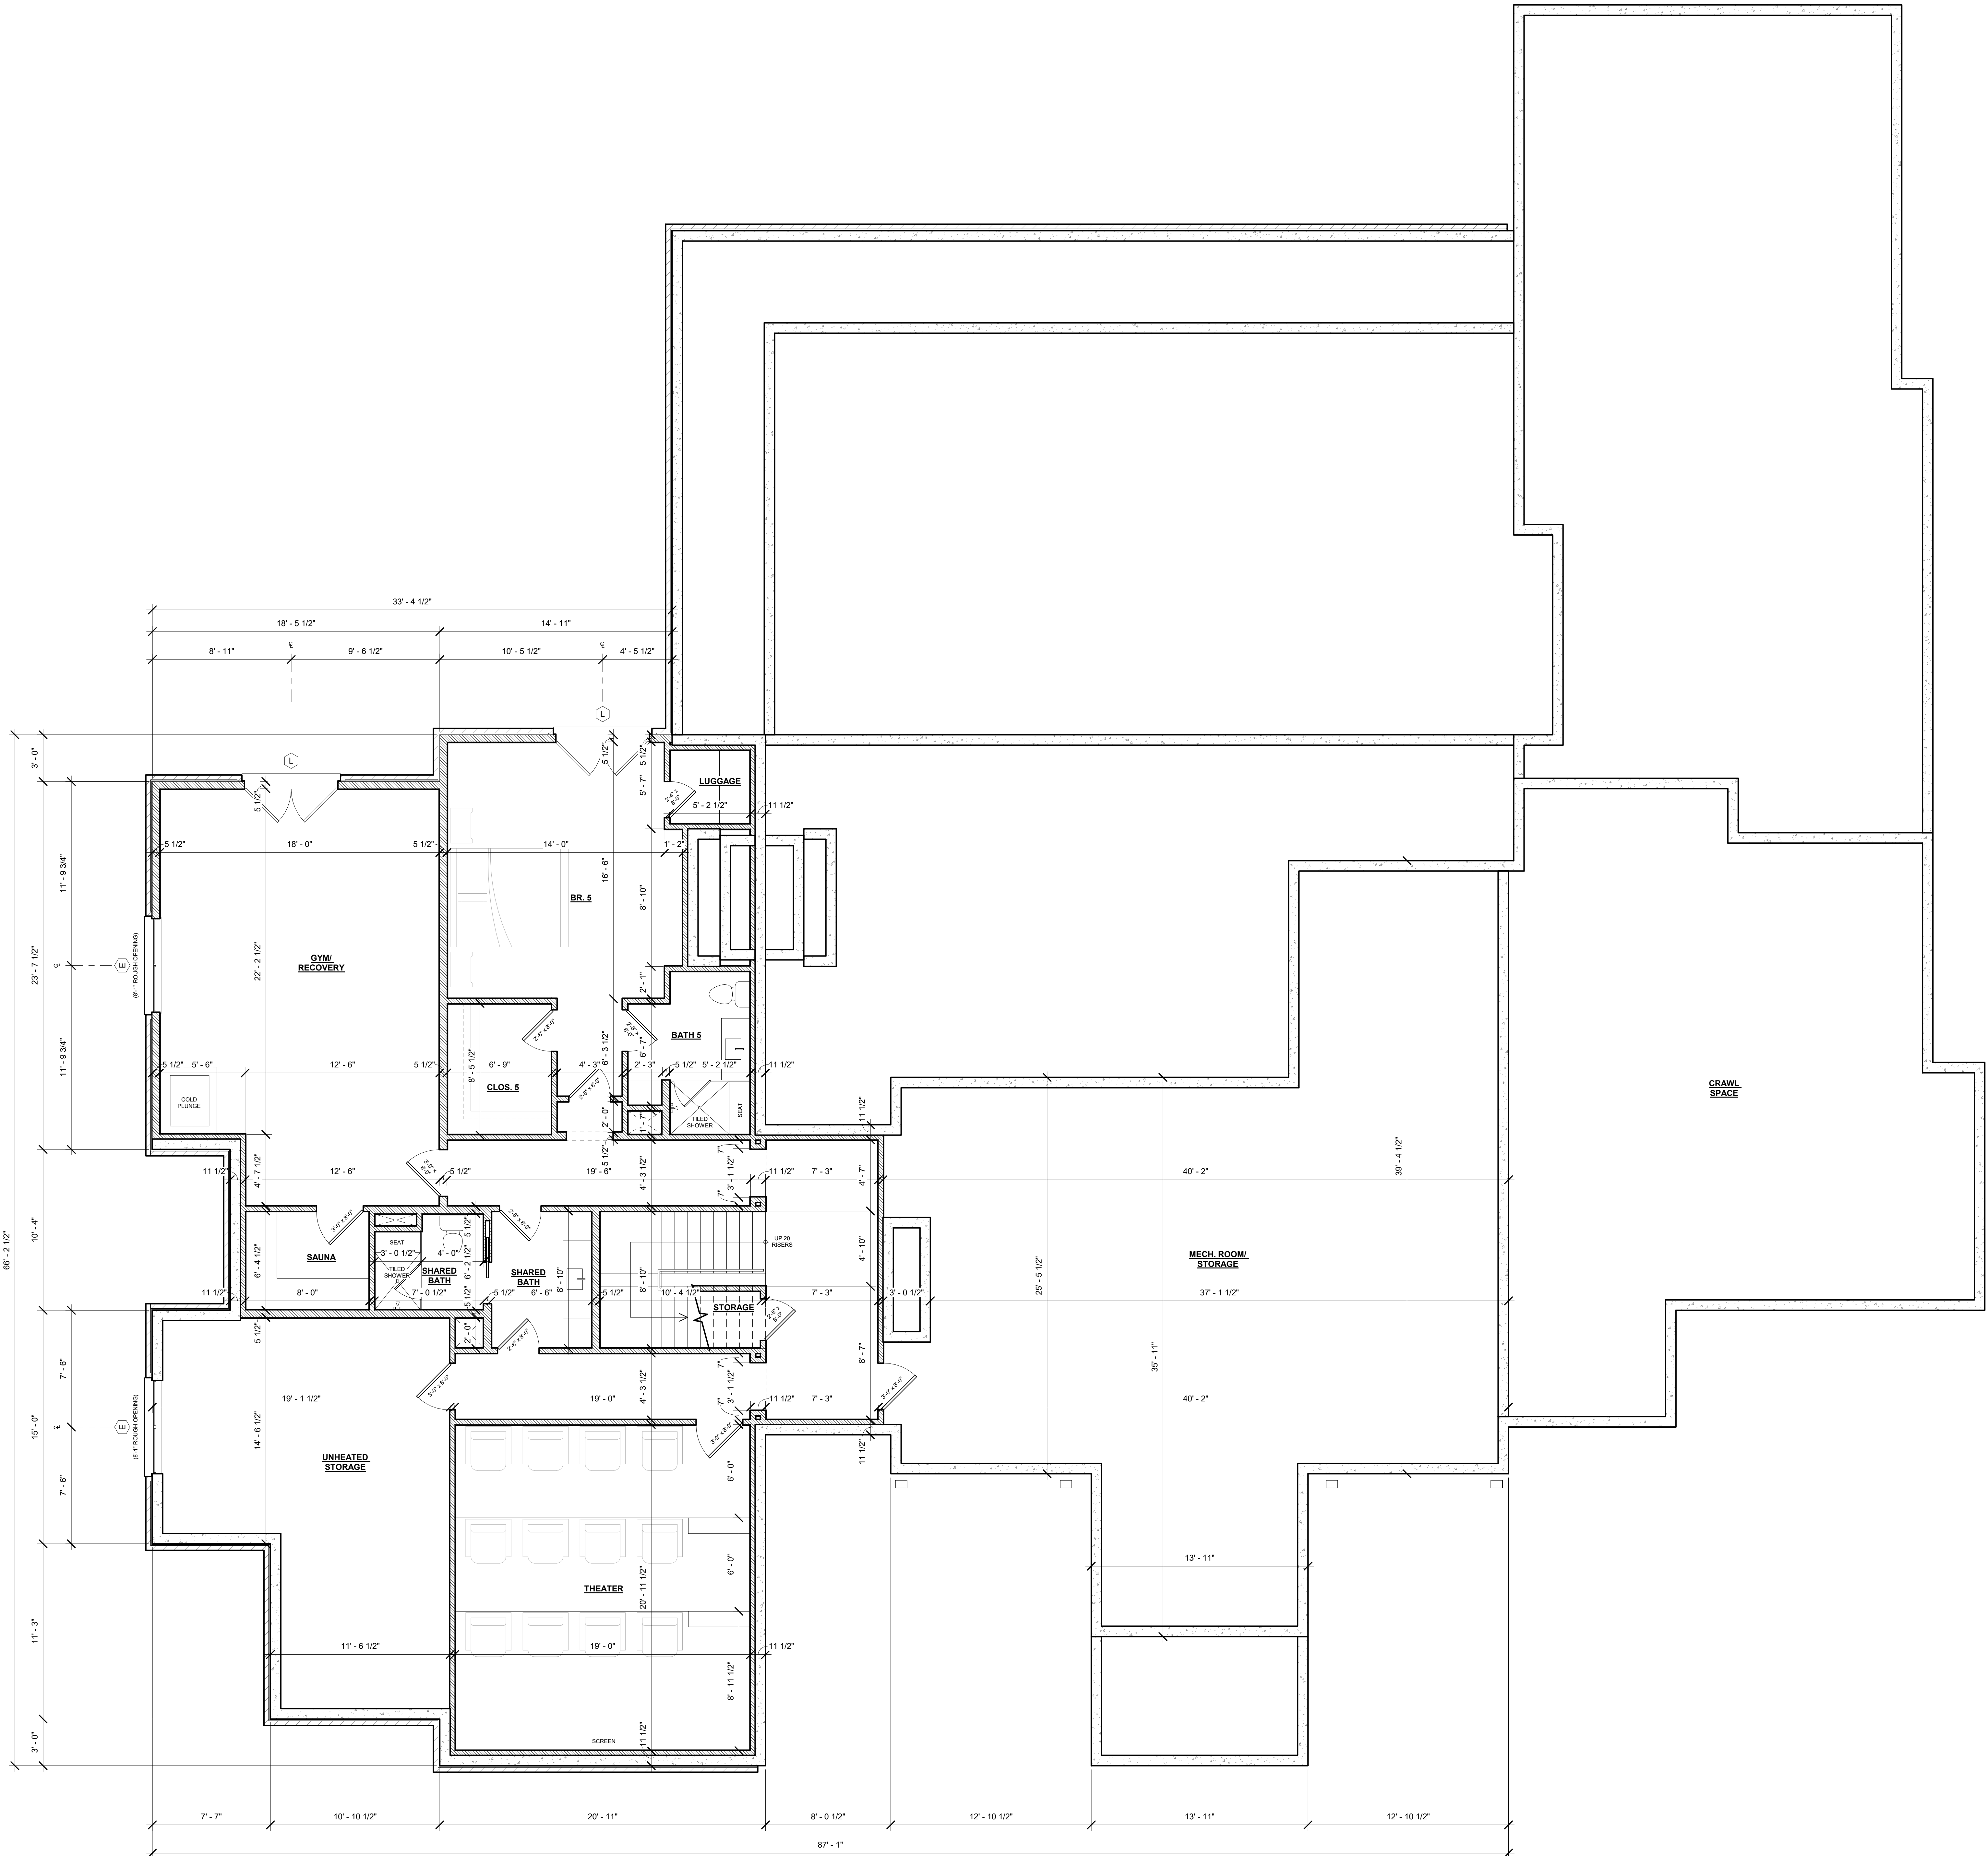

Window & Exterior Door Schedule						
Type Mark	# of Door/Window Panels	Width	Height	Transom Height	Window/Door Type	Comments
A	(2)	4' - 0"	9' - 0"	3' - 0"	French Doors	See Floor Plans for Door Operation
B	(1)	4' - 0"	6' - 0"	3' - 0"	Fixed Window	
C	(2)	4' - 0"	6' - 0"	3' - 0"	Fixed Windows	Factory Mullied
C1	(2)	4' - 0"	6' - 0"	3' - 0"	Casement Windows	Factory Mullied, Egress Windows
D	(1)	2' - 4"	4' - 6"		Fixed Window	
E	(2)	3' - 0"	6' - 0"		Fixed Windows	<varies>
E1	(2)	3' - 0"	6' - 0"		Casement Windows	Factory Mullied, Egress Windows
F	(1)	3' - 0"	8' - 0"		French Door	See Floor Plans for Door Operation
G	(1)	3' - 0"	8' - 0"		Half Glass Door	See Floor Plans for Door Operation
H	(2)	3' - 0"	5' - 0"		Fixed Windows	Factory Mullied
I	(4)	3' - 0"	9' - 0"		Fixed Windows	Factory Mullied
J	(4)	3' - 0"	9' - 0"		French Sliders	See Floor Plan for Door Operation
K	(6)	3' - 0"	9' - 0"		French Pockets	See Floor Plan for Door Operation
L	(2)	3' - 0"	8' - 0"		French Doors	See Floor Plans for Door Operation
M	(1)	4' - 0"	6' - 0"		Fixed Window	
M2	(1)	4' - 0"	6' - 0"		Fixed Window	Tempered Glazing
N	(1)	3' - 0"	6' - 0"		Fixed Window	
O	(1)	2' - 0"	4' - 0"		Fixed Window	

BASEMENT FLOOR PLAN
SCALE: 1/4" = 1'-0"

NOTE:
SEE FRAMING PACKAGE FOR ALL JOIST ORIENTATION AND SPACING.
TYPICAL ALL LOCATIONS.
SUPPLEMENT AND SIZE BEAMS PER STRUCTURAL ENGINEER.



ak designs
205 Powell Place, Suite 119
Brentwood, TN 37027

DESIGN DEVELOPMENT
not for construction

This document is an instrument of service and shall remain the property of AK DESIGN unless otherwise stated. It contains confidential information and shall not be reproduced, copied, or distributed without the written consent of AK DESIGN.

Copyright © 2026
ak designs

CAMPBELL RESIDENCE


Lot 1213 in Troubadour
College Grove, Tennessee

Basement Plan

Revision Date:

1.	
2.	
3.	
4.	
5.	
6.	

Project Number: A21018
Date: 07.23.26
Scale: 1/4" = 1'-0"

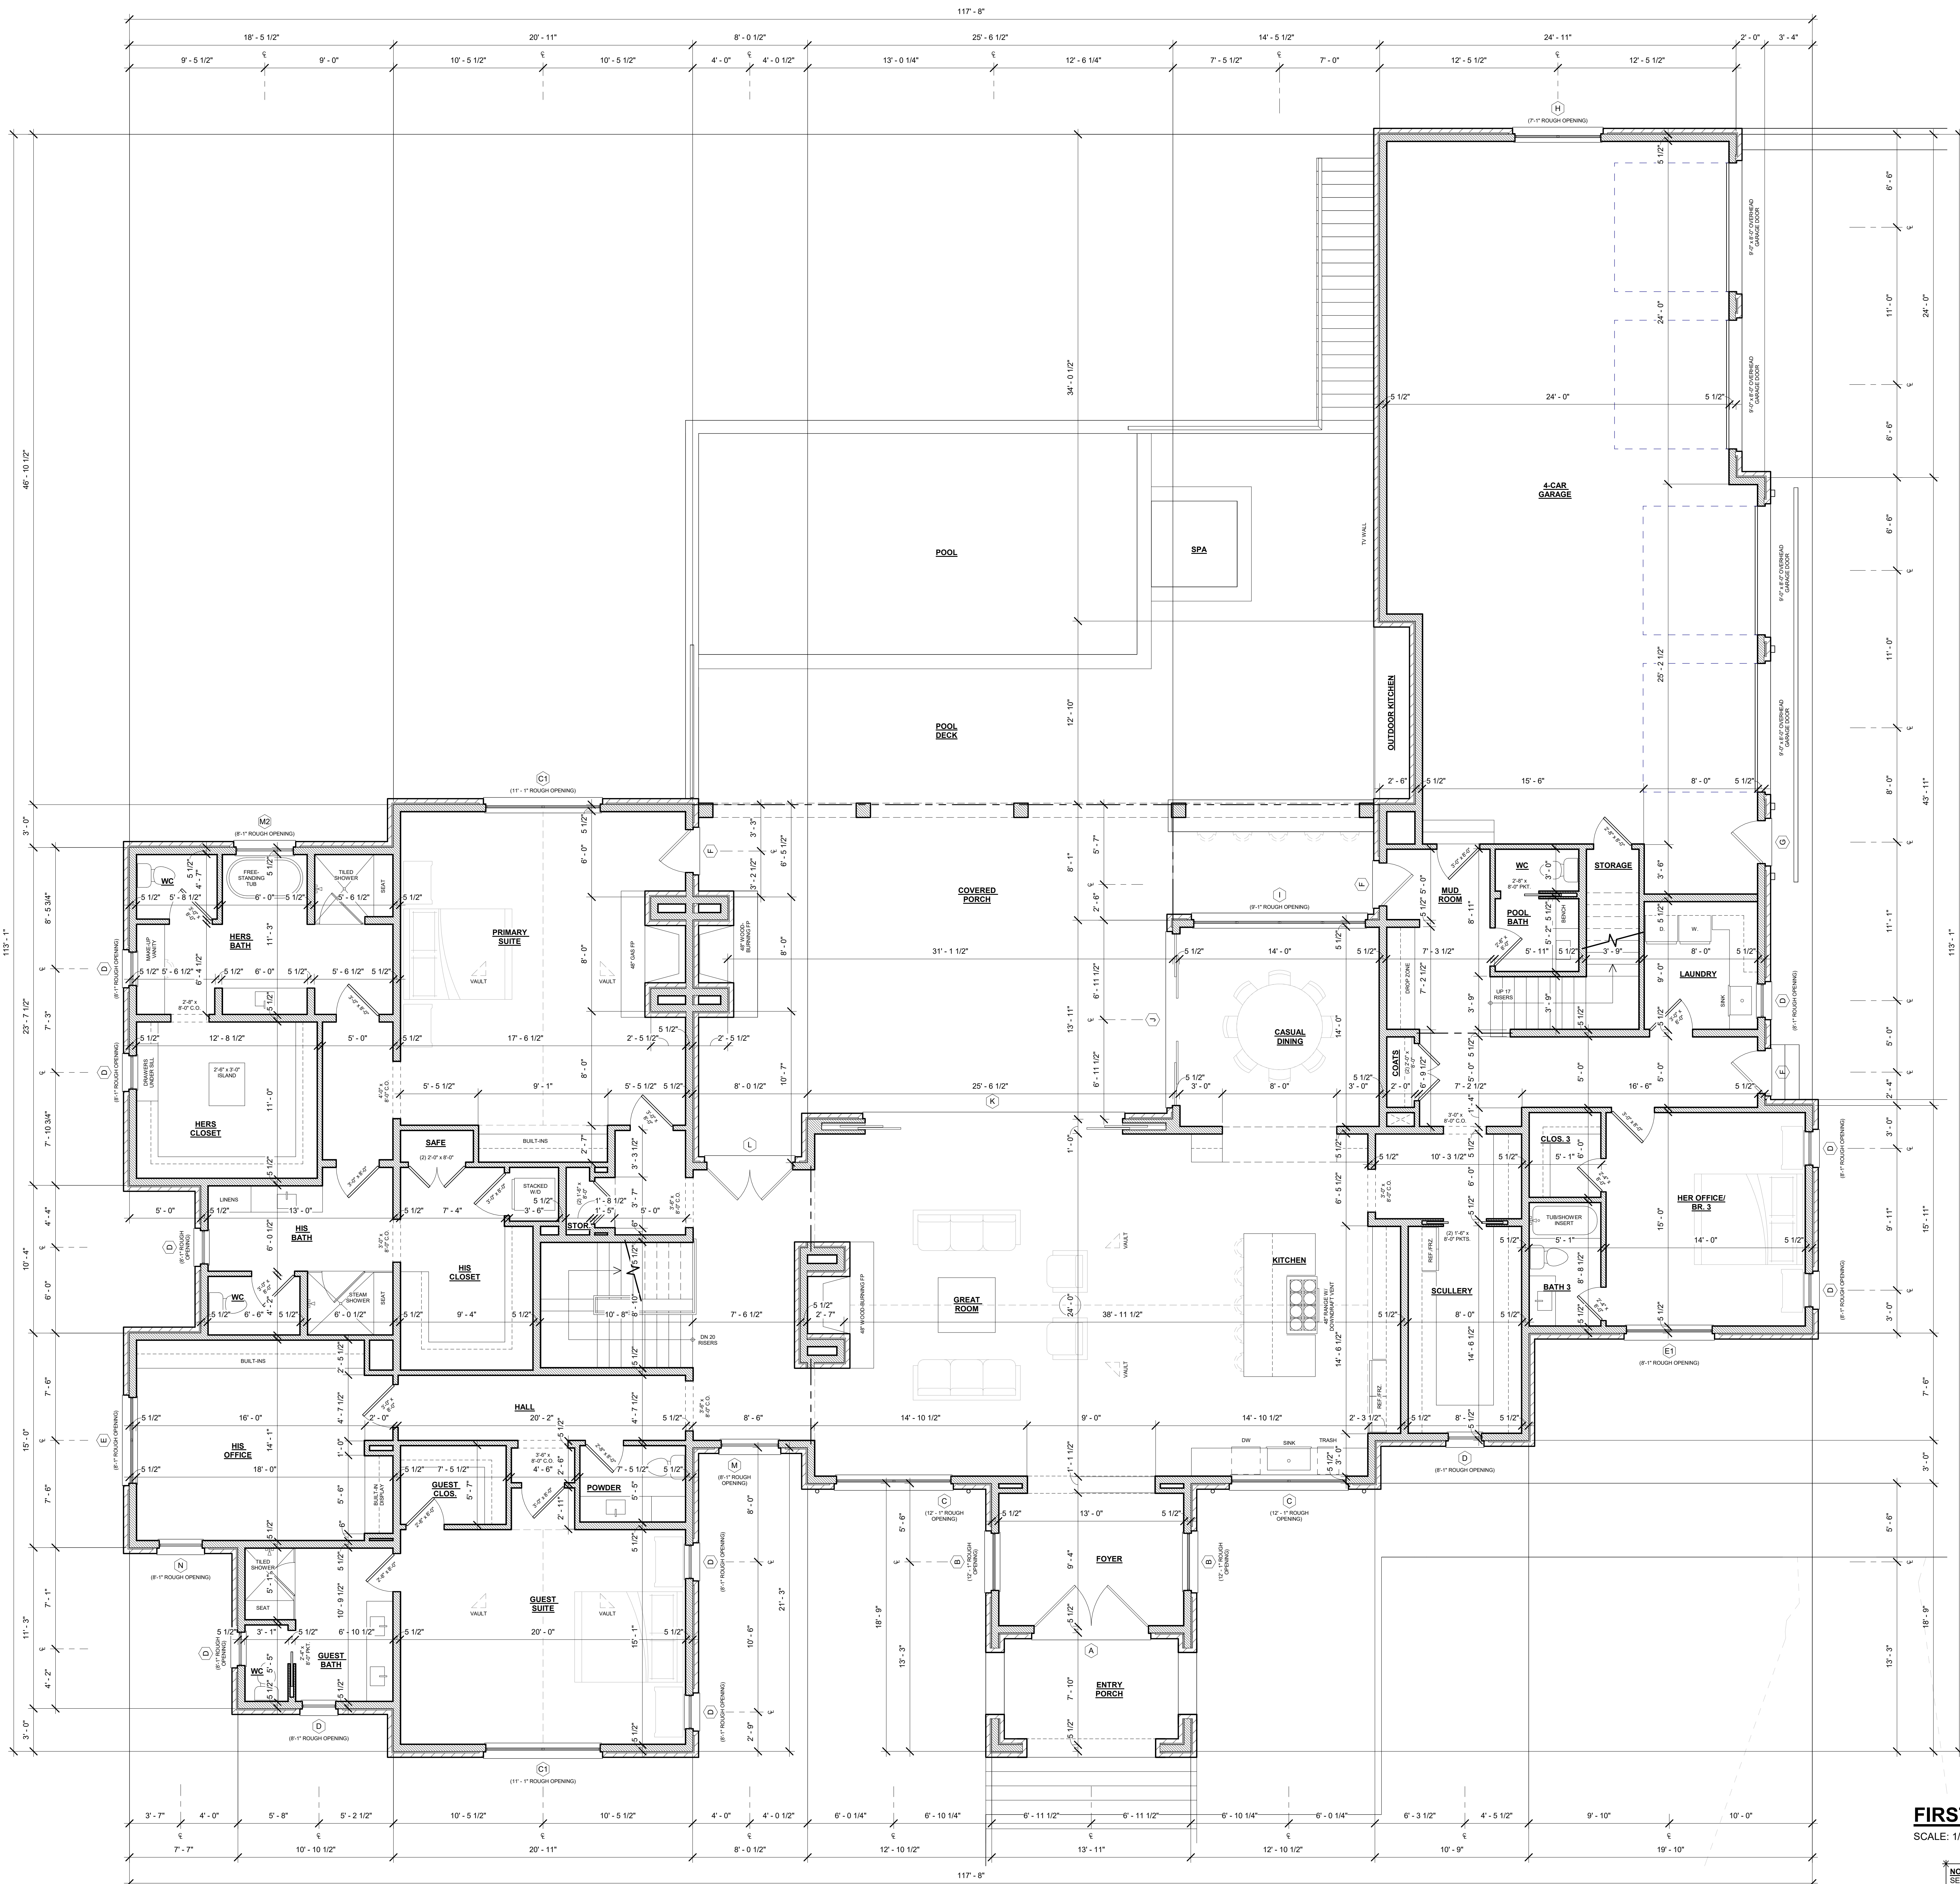


FIRST FLOOR PLAN
SCALE: 1/4" = 1'-0"

NOTE:
SEE FRAMING PACKAGE FOR ALL
JOIST ORIENTATION AND SPACING.
TYPICAL ALL LOCATIONS
SUPPLEMENT AND SIZE BEAMS PER
STRUCTURAL ENGINEER.

Window & Exterior Door Schedule						
Type Mark	# of Door/Window Panels	Width	Height	Transom Height	Window/Door Type	Comments
A	(2)	4'-0"	9'-0"	3'-0"	French Doors	See Floor Plans for Door Operation
B	(1)	4'-0"	6'-0"	3'-0"	Fixed Window	
C	(2)	4'-0"	6'-0"	3'-0"	Fixed Windows	Factory Mullied
C1	(2)	4'-0"	6'-0"	3'-0"	Casement Windows	Factory Mullied, Egress Windows
D	(1)	2'-4"	4'-6"		Fixed Window	
E	(2)	3'-0"	6'-0"		Fixed Windows	<varies>
E1	(2)	3'-0"	6'-0"		Casement Windows	Factory Mullied, Egress Windows
F	(1)	3'-0"	8'-0"		French Door	See Floor Plans for Door Operation
G	(1)	3'-0"	8'-0"		Half Glass Door	See Floor Plans for Door Operation
H	(2)	3'-0"	5'-0"		Fixed Windows	Factory Mullied
I	(4)	3'-0"	9'-0"		Fixed Windows	Factory Mullied
J	(4)	3'-0"	9'-0"		French Sliders	See Floor Plan for Door Operation
K	(6)	3'-0"	9'-0"		French Pockets	See Floor Plan for Door Operation
L	(2)	3'-0"	8'-0"		French Doors	See Floor Plans for Door Operation
M	(1)	4'-0"	6'-0"		Fixed Window	
M2	(1)	4'-0"	6'-0"		Fixed Window	Tempered Glazing
N	(1)	3'-0"	6'-0"		Fixed Window	
O	(1)	2'-0"	4'-0"		Fixed Window	

SQUARE FOOTAGE (O.F.S.)	
SQUARE FOOTAGE TAKEN FROM OUTSIDE FACE OF STUD	
HEATED	
BASEMENT	1,967 SF
FIRST FLOOR	4,619 SF
BEDROOM 3 APARTMENT	688 SF
	7,274 SF
UNHEATED	
4-CAR GARAGE	1,270 SF
ENTRY PORCH	88 SF
COVERED PORCH	959 SF
UNCONDITIONED STORAGE	410 SF
	2,728 SF
TOTAL UNDER ROOF	10,000 SF

- GENERAL NOTES**
- CONTRACTOR TO VERIFY ALL STRUCTURAL CONDITIONS WITH LICENSED STRUCTURAL ENGINEER PRIOR TO CONSTRUCTION. STRUCTURAL INFORMATION WITHIN IS INTENDED FOR DESIGN CONSIDERATION ONLY.
 - CONTRACTOR TO ENSURE COMPLIANCE OF CONSTRUCTION WITH ALL UPDATED, APPLICABLE BUILDING CODES.
 - CONTRACTOR TO ENSURE ADEQUATE CONSTRUCTION OF ALL NON-STRUCTURAL ELEMENTS INCLUDING, BUT NOT LIMITED TO: MATERIALS SEPARATION, FLOORING MATERIAL DIMENSION, INSULATION, TERMITE TREATMENT, PROPER DRAINAGE ETC.
 - DIMENSIONS ARE SHOWN FROM OUTSIDE FACE OF STUD AND CENTERLINES OF OPENINGS, UNLESS NOTED OTHERWISE.
 - CONTRACTOR TO ASSESS RELATIONSHIP OF ACTUAL FINISH FLOOR HEIGHT TO GRADE AND COORDINATE EGRESS AS REQUIRED BY CODE. CONTRACTOR SHALL CONTACT DESIGNER TO ADDRESS DESIGN INTENT WHERE APPLICABLE.
 - SUBSTITUTION OF FOUNDATION SYSTEMS SHALL BE COORDINATED TO ENSURE DESIGN INTENT (I.E. FINISH FLOOR MATERIAL, RELATIONSHIPS, ETC.) IS PRESERVED AND TO CONFORM WITH LOCAL BUILDING CODES.

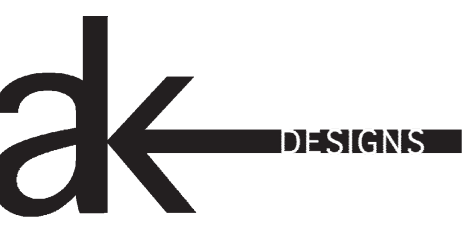

ak designs
205 Powell Place, Suite 119
Brentwood, TN 37027

DESIGN DEVELOPMENT
not for construction

This document is an instrument of service and shall remain the property of ak designs who reserve all common law, statutory and other reserved rights, including the copyright therein.
Copyright © 2026
ak designs

CAMPBELL RESIDENCE

Lot 1213 in Troubadour
College Grove, Tennessee

First Floor Plan

Revision Date:

1.	
2.	
3.	
4.	
5.	
6.	


Project Number: A21018

Date: 07.23.26

Scale: 1/4" = 1'-0"

Sheet

A102

 

Window & Exterior Door Schedule						
Type Mark	# of Door/Window Panels	Width	Height	Transom Height	Window/Door Type	Comments
A	(2)	4' - 0"	9' - 0"	3' - 0"	French Doors	See Floor Plans for Door Operation
B	(1)	4' - 0"	6' - 0"	3' - 0"	Fixed Window	
C	(2)	4' - 0"	6' - 0"	3' - 0"	Fixed Windows	Factory Mullied
C1	(2)	4' - 0"	6' - 0"	3' - 0"	Casement Windows	Factory Mullied, Egress Windows
D	(1)	2' - 4"	4' - 6"		Fixed Window	
E	(2)	3' - 0"	6' - 0"		Fixed Windows	<varies>
E1	(2)	3' - 0"	6' - 0"		Casement Windows	Factory Mullied, Egress Windows
F	(1)	3' - 0"	8' - 0"		French Door	See Floor Plans for Door Operation
G	(1)	3' - 0"	8' - 0"		Half Glass Door	See Floor Plans for Door Operation
H	(2)	3' - 0"	5' - 0"		Fixed Windows	Factory Mullied
I	(4)	3' - 0"	9' - 0"		Fixed Windows	Factory Mullied
J	(4)	3' - 0"	9' - 0"		French Sliders	See Floor Plan for Door Operation
K	(6)	3' - 0"	9' - 0"		French Pockets	See Floor Plan for Door Operation
L	(2)	3' - 0"	8' - 0"		French Doors	See Floor Plans for Door Operation
M	(1)	4' - 0"	6' - 0"		Fixed Window	
M2	(1)	4' - 0"	6' - 0"		Fixed Window	Tempered Glazing
N	(1)	3' - 0"	6' - 0"		Fixed Window	
O	(1)	2' - 0"	4' - 0"		Fixed Window	

SECOND FLOOR PLAN
SCALE: 1/4" = 1'-0"

NOTE:
SEE FRAMING PACKAGE FOR ALL
JOIST ORIENTATION AND SPACING.
TYPICAL ALL LOCATIONS.
SUPPLEMENT AND SIZE BEAMS PER
STRUCTURAL ENGINEER.



ak designs
205 Powell Place, Suite 119
Brentwood, TN 37027

DESIGN
DEVELOPMENT
not for construction

This document is an instrument of service and shall remain the property of ak designs who reserve all common law, statutory and other reserved rights, including the copyright therein.

Copyright © 2026
ak designs

CAMPBELL RESIDENCE

Lot 1213 in Troubadour
College Grove, Tennessee

Second Floor Plan

Revision Date:

1.	
2.	
3.	
4.	
5.	
6.	

Project Number: A21018

Date: 07.23.26

Scale: 1/4" = 1'-0"

Sheet

A103

TYPICAL INSULATION LOCATIONS:

1. EXTERIOR WALLS DIRECTLY ADJACENT TO CONDITIONED SPACE
2. ROOF RAFTERS DIRECTLY ADJACENT TO CONDITIONED SPACE
3. INTERIOR WALLS SEPARATING CONDITIONED SPACE FROM UNCONDITIONED SPACE
4. FLOOR JOISTS SEPARATING CONDITIONED SPACE FROM UNCONDITIONED SPACE

TYPICAL FLASHING APPLICATION:

1. WINDOWS AND DOORS CONTRACTOR TO ENSURE COMPLIANCE OF CONSTRUCTION WITH ALL UPDATED, APPLICABLE BUILDING CODES.
2. ALL HORIZONTAL MATERIAL CHANGES
3. SIDES OF DORMERS
4. SIDES OF WALLS AT INTERSECTING ROOF LINES
5. CHIMNEY/ROOF INTERSECTIONS
6. PORCH ROOF, DECK AND WALL INTERSECTIONS
7. ABOVE CORNICE RETURNS
8. SKIRT ASSEMBLIES
9. ANY OTHER FACADE PENETRATIONS (E.G. FDN. VENTS GABLE VENTS, ETC.)

**FRONT ELEVATION**
SCALE: 1/4" = 1'-0"**LEFT ELEVATION**
SCALE: 1/4" = 1'-0"

Front & Left Elevations

Revision Date:

1.	
2.	
3.	
4.	
5.	
6.	

Project Number: A21018
Date: 07.23.26
Scale: 1/4" = 1'-0"

CAMPBELL RESIDENCE

Lot 1213 in Troubadour
College Grove, Tennessee

Right & Rear Elevations

Revision Date:

1.	
2.	
3.	
4.	
5.	
6.	

Project Number: A21018
Date: 07.23.26
Scale: 1/4" = 1'-0"


Sheet

TYPICAL INSULATION LOCATIONS:

- EXTERIOR WALLS DIRECTLY ADJACENT TO CONDITIONED SPACE
- ROOF RAFTERS DIRECTLY ADJACENT TO CONDITIONED SPACE
- INTERIOR WALLS SEPARATING CONDITIONED SPACE FROM UNCONDITIONED SPACE
- FLOOR JOISTS SEPARATING CONDITIONED SPACE FROM UNCONDITIONED SPACE

TYPICAL FLASHING APPLICATION:

- WINDOWS AND DOORS CONTRACTOR TO ENSURE COMPLIANCE OF CONSTRUCTION WITH ALL UPDATED, APPLICABLE BUILDING CODES.
- ALL HORIZONTAL MATERIAL CHANGES
- SIDES OF DORMERS
- SIDES OF WALLS AT INTERSECTING ROOF LINES
- CHIMNEY/ROOF INTERSECTIONS
- PORCH ROOF, DECK AND WALL INTERSECTIONS
- ABOVE CORNICE RETURNS
- SKIRT ASSEMBLIES
- ANY OTHER FACADE PENETRATIONS (E.G. FDN. VENTS GABLE VENTS, ETC.)

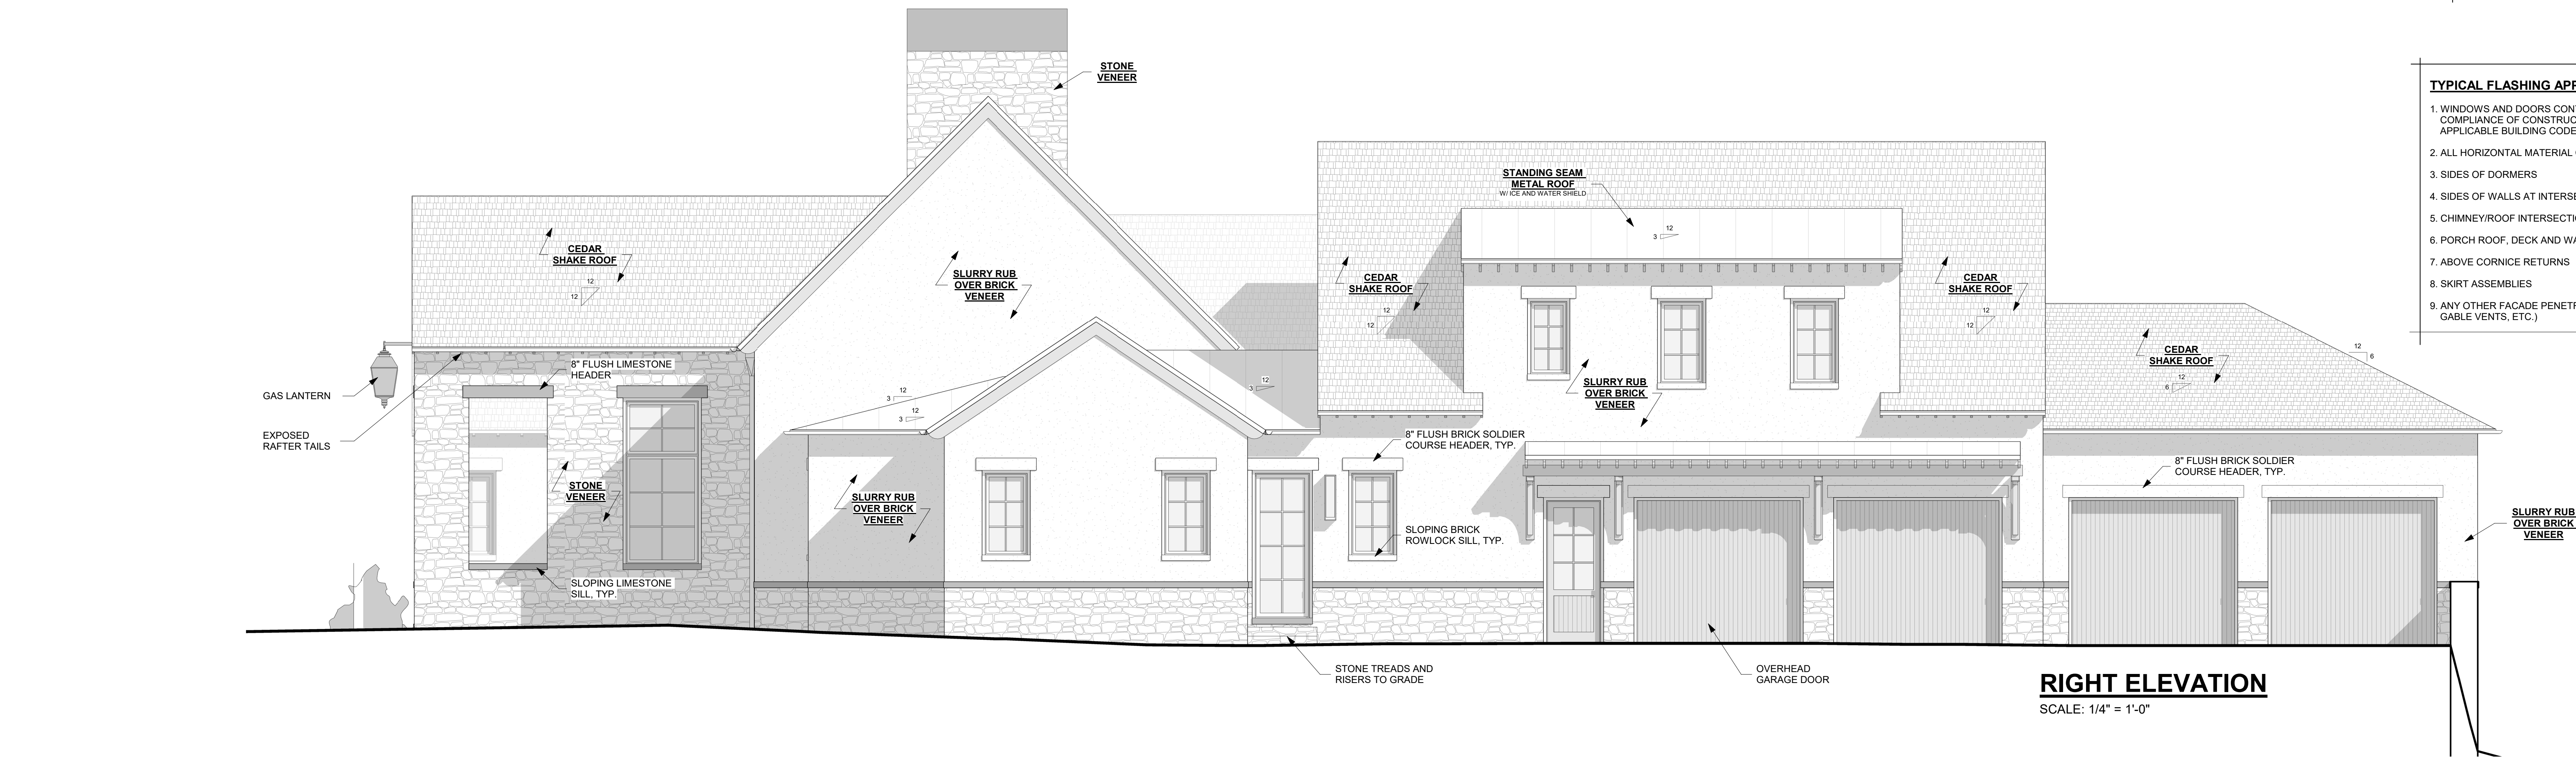



- TYPICAL INSULATION LOCATIONS:**
1. EXTERIOR WALLS DIRECTLY ADJACENT TO CONDITIONED SPACE
 2. ROOF RAFTERS DIRECTLY ADJACENT TO CONDITIONED SPACE
 3. INTERIOR WALLS SEPARATING CONDITIONED SPACE FROM UNCONDITIONED SPACE
 4. FLOOR JOISTS SEPARATING CONDITIONED SPACE FROM UNCONDITIONED SPACE

- TYPICAL FLASHING APPLICATION:**
1. WINDOWS AND DOORS CONTRACTOR TO ENSURE COMPLIANCE OF CONSTRUCTION WITH ALL UPDATED, APPLICABLE BUILDING CODES.
 2. ALL HORIZONTAL MATERIAL CHANGES
 3. SIDES OF DORMERS
 4. SIDES OF WALLS AT INTERSECTING ROOF LINES
 5. CHIMNEY/ROOF INTERSECTIONS
 6. PORCH ROOF, DECK AND WALL INTERSECTIONS
 7. ABOVE CORNICE RETURNS
 8. SKIRT ASSEMBLIES
 9. ANY OTHER FACADE PENETRATIONS (E.G. FDN. VENTS GABLE VENTS, ETC.)

ROOF PLAN
SCALE: 1/4" = 1'-0"



ak designs
205 Powell Place, Suite 119
Brentwood, TN 37027

**DESIGN
DEVELOPMENT**
not for construction

This document is an instrument of service and shall remain the property of AK DESIGN who retains all common law, statutory and other reserved rights, including the copyright therein.

Copyright © 2026
ak designs

CAMPBELL RESIDENCE

Lot 1213 in Troubadour
College Grove, Tennessee

Roof Plan

Revision Date:

1.	
2.	
3.	
4.	
5.	
6.	

Project Number: A21018
Date: 07.23.26
Scale: 1/4" = 1'-0"

Sheet
A501