


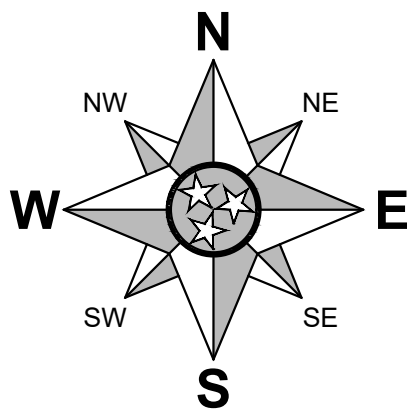

GPS SURVEY DATA INFORMATION:


- TYPE OF GPS SURVEY: RTK
- POSITIONAL ACCURACY: 0.07 FEET
- DATUM/EPOCH: NAD83 (2011) EPOCH 2010.00
- PUBLISHED/FIXED CONTROL USED: TGRN
- GEOID MODEL: GEOID 18
- COMBINED GRID SCALE FACTOR: 0.99991572
- UNITS: (US FEET)(GRID)

SUBJECT PROPERTY INFORMATION:

- OWNER: ARRINGTON PROPERTY HOLDINGS, LLC
- TAX MAP 136F, GROUP G, PARCEL 6.00
- INSTRUMENT: DB 9820, PG 452
- PLAT INSTRUMENT: PB 85, PG 148
- LOT 1213, TROUBADOUR - SECTION 12B
- TOTAL AREA = 0.90 AC (39,108 SF)±

CURVE TABLE				
CURVE #	LENGTH	RADIUS	CHORD BRNG	CHORD LENGTH
C1	55.03	495.00	N12° 59' 44"W	55.00
C2	83.63	480.00	N11° 11' 22"W	83.52

LINE TABLE		
LINE #	LENGTH	DIRECTION
L1	50.60	S73° 11' 25"E
L2	42.95	S27° 34' 05"E
L3	40.95	S06° 38' 12"W
L4	35.73	S06° 50' 50"E
L5	17.96	S22° 51' 59"E
L6	23.66	N16° 10' 50"W

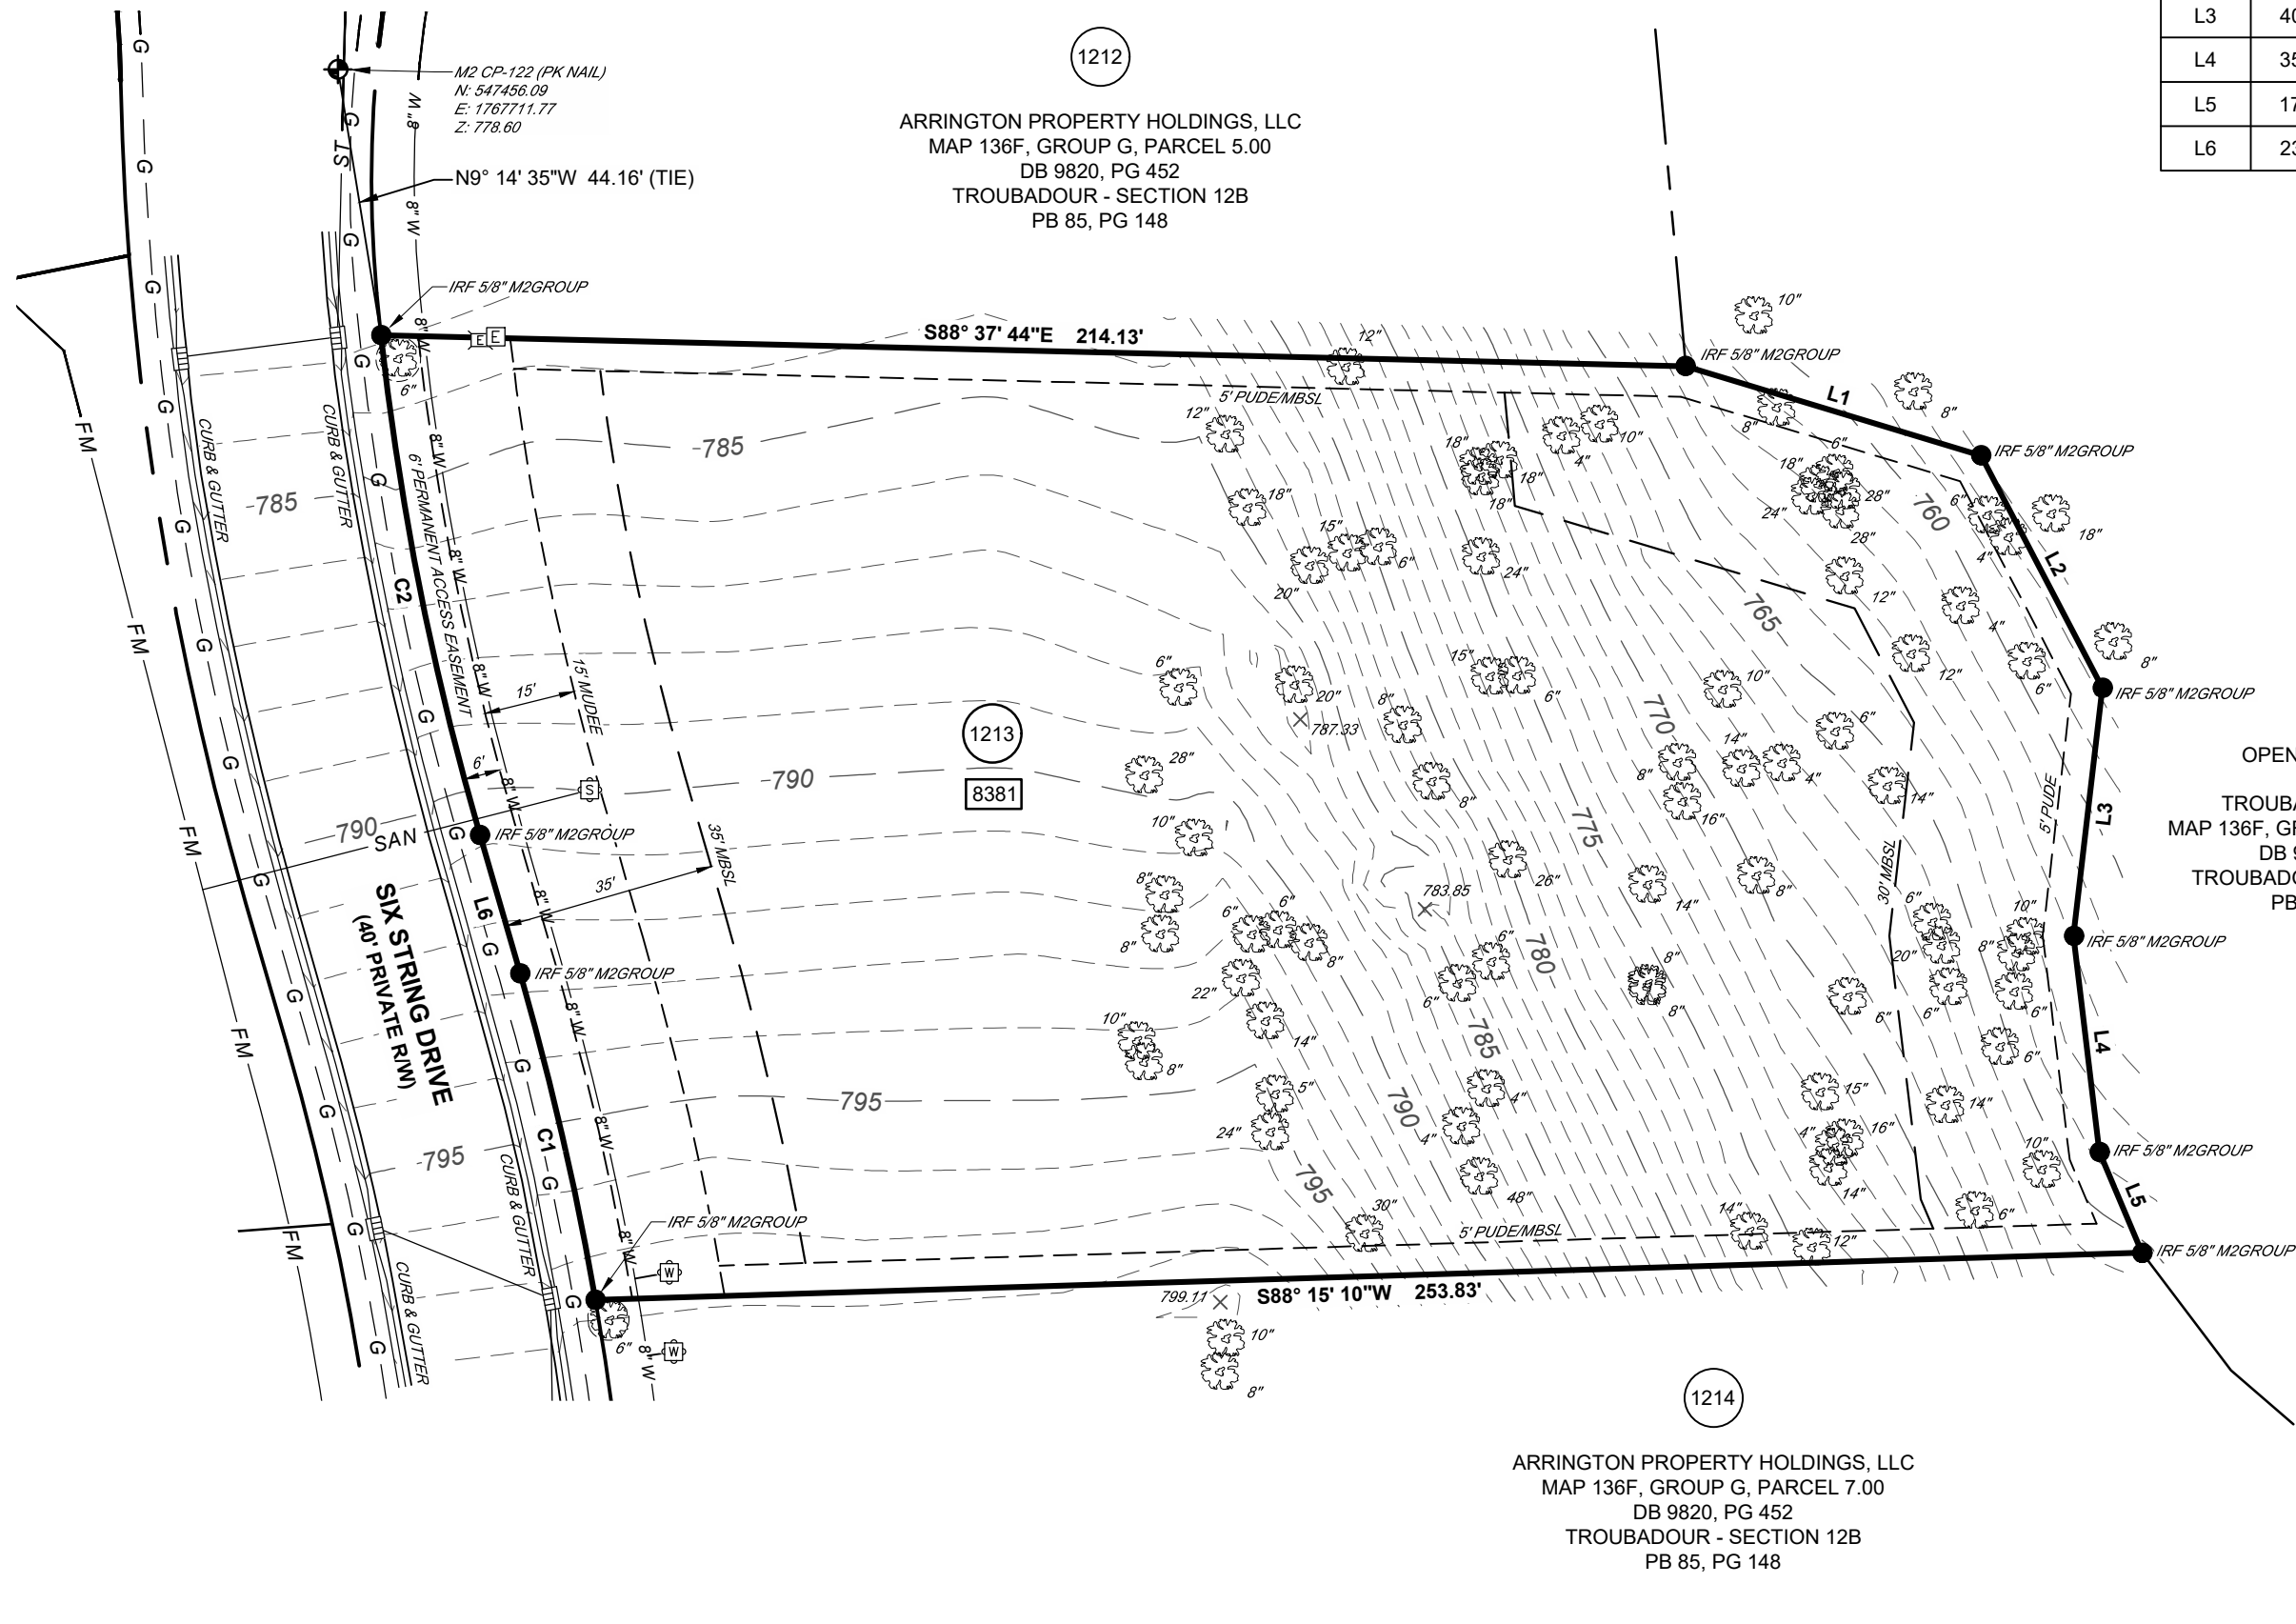


GENERAL NOTES:

1. BEARINGS ARE BASED ON THE TENNESSEE STATE PLANE COORDINATE SYSTEM (NAD83, 2011).
2. ELEVATIONS ARE REFERENCED TO THE NORTH AMERICAN VERTICAL DATUM OF 1988 (NAVD88, GEOID 18). CONTOURS ARE SHOWN AT 1-FOOT INTERVALS.
3. THE FIELD SURVEY WAS COMPLETED ON MARCH 21, 2026.
4. THIS SURVEY WAS PREPARED USING THE CURRENT DEEDS AND PLATS OF RECORD.
5. ALL DEED BOOK AND PLAT REFERENCES PERTAIN TO THE REGISTER'S OFFICE FOR WILLIAMSON COUNTY, TENNESSEE.
6. ADJOINING PROPERTY LINES SHOWN WERE PLOTTED FROM INFORMATION TAKEN FROM EITHER DEED DESCRIPTION, RECORD PLATS, OR TAX MAPS.
7. UTILITIES SHOWN HEREON WERE COMPILED FROM VISIBLE STRUCTURES AT THE SITE, INFORMATION FROM PLANS, AND PHYSICAL MARKINGS AND COMBINED TO DEVELOP A VIEW OF THE UNDERGROUND UTILITIES. HOWEVER, LACKING EXCAVATION, THE EXACT LOCATION OF UNDERGROUND FEATURES CANNOT BE ACCURATELY, COMPLETELY, AND RELIABLY DEPICTED. IN ADDITION, IN SOME JURISDICTIONS, 811 OR OTHER SIMILAR UTILITY LOCATE REQUESTS FROM SURVEYORS MAY BE IGNORED OR RESULT IN AN INCOMPLETE RESPONSE. THIS SURVEYOR MAKES NO GUARANTEE THAT THE UNDERGROUND UTILITIES SHOWN COMPRISE ALL SUCH UTILITIES IN THE AREA, EITHER IN SERVICE OR ABANDONED. THIS SURVEYOR FURTHER DOES NOT WARRANT THAT THE UNDERGROUND UTILITIES SHOWN ARE IN THE EXACT LOCATION INDICATED. VERIFICATION OF EXISTENCE, LOCATIONS, AND DEPTH SHOULD BE MADE BEFORE CONDUCTING ANY EXCAVATION IN THE VICINITY OF THE UTILITY.
8. THE PROPERTY SHOWN HEREON IS LOCATED IN A FLOOD HAZARD ZONE "X" (AREAS DETERMINED TO BE OUTSIDE OF THE 0.2% ANNUAL CHANCE FLOODPLAIN) ACCORDING TO F.I.R.M. MAP "WILLIAMSON COUNTY, TENNESSEE" PANEL 385 OF 485, MAP NUMBER 47187C0385G, EFFECTIVE DECEMBER 20, 2024.
9. THE SUBJECT PROPERTY IS CURRENTLY ZONED "RD-1" (RURAL DEVELOPMENT DISTRICT 1), BASED ON THE OFFICIAL ZONING MAP FOR WILLIAMSON COUNTY, TENNESSEE. A CURRENT ZONING REPORT AND/OR ZONING LETTER HAS NOT BEEN PROVIDED TO THE SURVEYOR. THE MINIMUM BUILDING SETBACK REQUIREMENTS FOR "RD-1" ZONING ARE AS FOLLOWS:
 - FRONT SETBACK = 35'
 - SIDE SETBACK = 5'
 - REAR SETBACK = 30'
10. MINIMUM BUILDING SETBACKS HAVE BEEN SHOWN AND NOTED HEREON PER WILLIAMSON COUNTY ZONING ORDINANCE, AS REFERENCED ABOVE.
11. NO TITLE REPORT WAS PROVIDED TO THIS SURVEYOR REGARDING THE SUBJECT PROPERTIES, THEREFORE, THIS SURVEY IS SUBJECT TO THE FINDING OR ANY OTHER FACTS THAT AN ACCURATE AND CURRENT TITLE SEARCH AND REPORT MY DISCLOSE.



SURVEYOR'S CERTIFICATE

I HEREBY CERTIFY THAT THE INFORMATION SHOWN HEREON IS TRUE AND ACCURATE TO THE BEST OF MY PROFESSIONAL KNOWLEDGE AND BELIEF. THE SURVEY SHOWN HEREON REPRESENTS A CATEGORY I SURVEY, HAVING A LINEAR ERROR OF CLOSURE WHICH IS EQUAL TO OR LESS THAN 1 FOOT PER 10,000 FEET OF LAND (1:10,000). THIS SURVEY WAS MADE IN COMPLIANCE WITH THE CURRENT TENNESSEE MINIMUM STANDARDS OF PRACTICE.

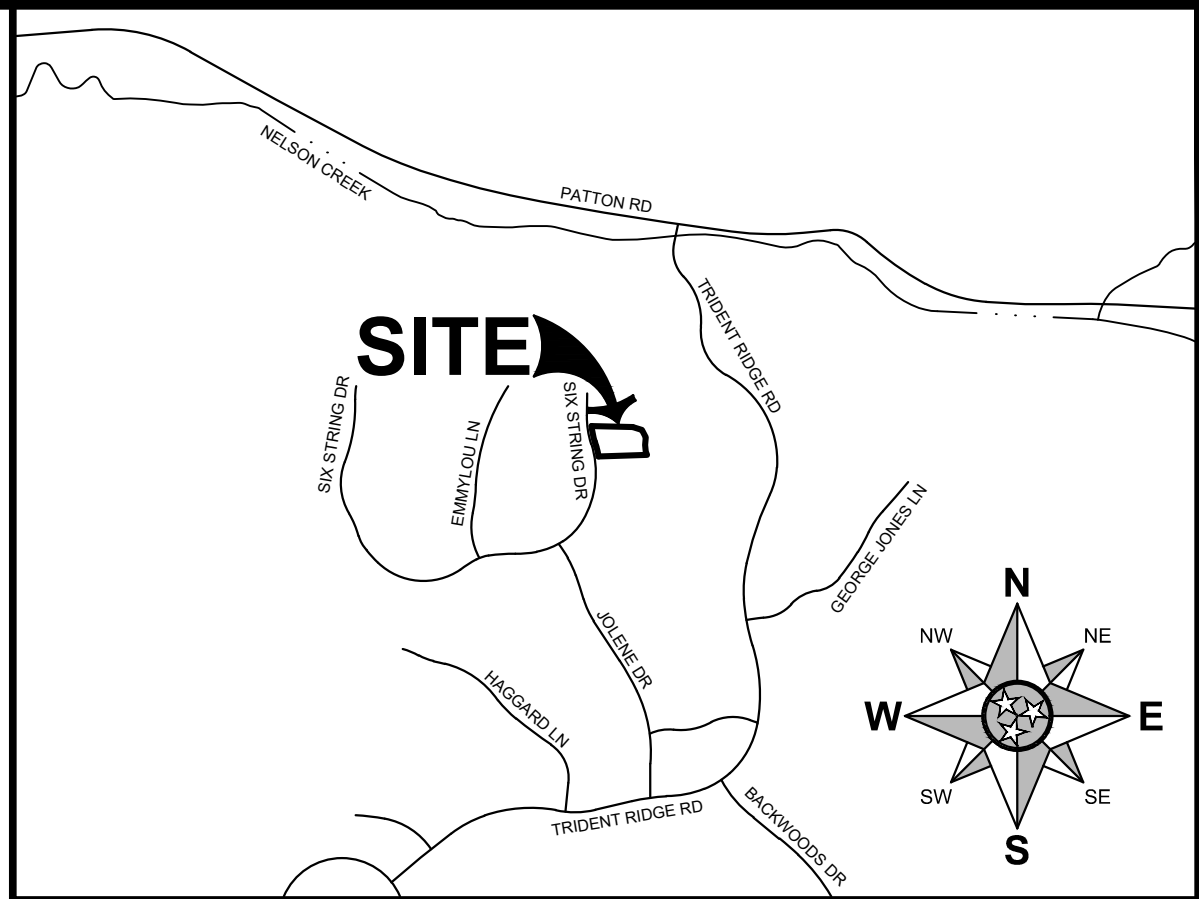

VICINITY MAP
SCALE: 1"=1000'

LEGEND:

	EXISTING PROPERTY LINE
	EXISTING RIGHT-OF-WAY
	EXISTING ADJACENT PROPERTY LINE
	EXISTING EASEMENT
	MBSL
	MINIMUM BUILDING SETBACK LINE
	EXISTING INDEX CONTOUR
	EXISTING INTERMEDIATE CONTOUR
	SAN
	EXISTING SANITARY SEWER LINE
	FM
	EXISTING FORCEMAIN LINE
	ST
	EXISTING STORM SEWER LINE
	G
	EXISTING GAS LINE
	W
	EXISTING WATER LINE
	IRON REBAR FOUND (IRF)
	BENCHMARK / SURVEY CONTROL
	WATER METER
	SEWER BOX
	CURB INLET
	ELECTRIC PULL BOX (FLUSH WITH GRADE)
	ELECTRIC CONTROL BOX (ON BUILDING)
	TREE, DECIDUOUS
	EXISTING SPOT ELEVATION
	MBSL
	MINIMUM BUILDING SETBACK LINE
	PUDE
	PUBLIC UTILITY & DRAINAGE EASEMENT
	EOP
	EDGE OF PAVEMENT
	1200
	LOT NUMBER
	911
	ADDRESS

REVISION #	DATE	DESCRIPTION
BOUNDARY & TOPOGRAPHIC SURVEY LOT 1213, TROUBADOUR - SECTION 12B 8381 SIX STRING DR 18TH CIVIL DISTRICT WILLIAMSON COUNTY, TENNESSEE		
DATE :	APRIL 2, 2026	DRAWN BY : ERG
PROJECT NUMBER :	26-095	CHECKED BY : SVH

M2 GROUP

P.O. BOX 2543
BRENTWOOD, TN 37024-2543
615-656-0257 / M2GROUPLLC.COM

SHEET NUMBER:

SV-01