



THE STONEHOUSE COMPANY

EXCLUSIVE OFF-MARKET PROPERTY



1055 ZOPHI ST.

Nashville TN 37216 · East Nashville

4

BEDROOMS

3.1

BATHROOMS

2,171

SQUARE FEET

1

CAR GARAGE

PROPERTY HIGHLIGHTS

- City Views
- Large Primary
- Walk In Closet
- High Ceilings
- Gated Front Yard
- Wet Bar

AT A GLANCE

PRICE

\$765,000

COMPLETION

August 2026

BUILDER

**Ark
Development**

AREA

**East
Nashville**


SCOPE OF WORK

THIS PROJECT INVOLVES THE DEMOLITION OF AN EXISTING STRUCTURE AND THE SUBDIVISION OF A SINGLE LOT INTO TWO SEPARATE PARCELS. ON EACH PARCEL, AN IDENTICAL, IMPROVED RESIDENCE WILL BE CONSTRUCTED. THE NEW RESIDENCES WILL BE 1.5 STORY HOMES FEATURING 10' CEILINGS ON THE FIRST AND SECOND FLOORS WITH THE EXCEPTION OF A 15' VALUED CEILING IN THE MASTER BEDROOM, AND ALSO AN 8TH FLOOR LOFT. THE FLOOR PLAN INCLUDES 4 BEDROOMS, 3 FULL BATHROOMS, AND 1 HALF BATHROOM.

THE STRUCTURES WILL BE FRAMED WITH 2X6 WOOD EXTERIOR WALLS ON CRAWLSPACE FOUNDATIONS. AT THE FRONT, EACH UNIT WILL FEATURE A 32'x52' FT. CONCRETE SLAB COVERED PORCH, AND AT THE REAR, A 14'x38' FT. UNCOVERED CONCRETE PATIO.

ALL ELECTRICAL, PLUMBING, AND MECHANICAL SYSTEMS WILL BE INSTALLED IN ACCORDANCE WITH APPLICABLE CODES, WITH FINAL INSPECTIONS AND PERMITS TO BE OBTAINED BY THE OWNER. STRUCTURE DEMOLITION, LOT SUBDIVISION, DRIVEWAY CONSTRUCTION, AND UTILITY SERVICE CONNECTIONS (PARKING, GRADING, AND LANDSCAPING) WILL BE COMPLETED IN COMPLIANCE WITH ALL LOCAL ZONING AND BUILDING REGULATIONS.

VICINITY MAP

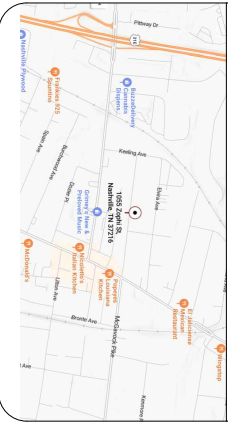

PROJECT DATA


PROPERTY CLASSIFICATION: 00 - RESIDENTIAL
PARCEL IDS: (UPDATED UPON SUBDIVISION)
ZONING CLASSIFICATION: R-1 LOW DENSITY ZONING DISTRICT
LOT DESCRIPTION: CASPER ZOPHI PLACE
SUBDIVISION: 0.08 (UNIT A) / 0.06 (UNIT B)
ACRES: 4
BEDROOMS: 4 (THIRD FLOOR IS A VALUED LOFT)
FULL BATHS: 3
HALF BATHS: 1
TOTAL HEATED AREA: 2,143 SQ. FT.
CRAWLSPACE: 120 SQ. FT.
CONCRETE PORCH (COVERED): 148 SQ. FT.
FOUNDATION: 148 SQ. FT.
CEILING HEIGHT: 10'-0" ON THE FIRST AND SECOND FLOORS HAVE 10'-0" CEILINGS, WITH THE EXCEPTION OF THE VALUED MASTER BEDROOM ON THE SECOND FLOOR AT 15'-0" THE LOFT LEVEL HAS 8'-0" CEILINGS THROUGHOUT.

ADOPTED BUILDING CODES

ALL CONSTRUCTION SHALL COMPLY WITH THE ADOPTED ORDINANCES AND POLICIES OF THE GOVERNING AGENCY HAVING JURISDICTION AND THE LATEST ADOPTED EDITIONS OF THE FOLLOWING:

INTERNATIONAL RESIDENTIAL CODE 2021 IRC
INTERNATIONAL MECHANICAL CODE 2021 IMC
INTERNATIONAL PLUMBING CODE 2021 IPC
NATIONAL ELECTRICAL CODE 2020 NEC
NATIONAL ELECTRICAL CODE 2021 NEC
INTERNATIONAL BUILDING CODE 2021 IBC
JOB CARD SHALL BE POSTED IN A CONSPICUOUS PLACE ON THE SITE AND READILY AVAILABLE FOR SIGNATURES.

DRAWING SYMBOLS

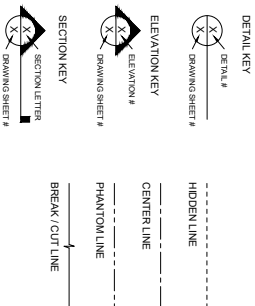

APPROVAL STAMP

PROJECT TEAM


PROPERTY OWNER: ADO HOLDINGS LLC
OWNER: ADO HOLDINGS LLC
PROJECT MANAGER: INVESTMENTS.DAM@GMAIL.COM
DESIGNER: DRAFT: CARY JACKSON
CONTACT: (423) 215-5607
PHONE: (423) 215-5607
EMAIL: INFO@DRAFTBYCARY.COM

DRAWING LEGEND

A0.0 COVER SHEET
A0.1 SITE PLAN
A2.0 CRAWLSPACE FLOOR PLAN
A2.1 EXTERIOR ELEVATIONS
A2.2 INTERIOR ELEVATIONS
A2.3 SECOND FLOOR PLAN
A2.4 LOFT FLOOR PLAN
A3.0 EXTERIOR ELEVATIONS
A3.1 INTERIOR ELEVATIONS
A5.0 ROOF PLAN
A5.1 SECTIONS
A6.0 ELECTRICAL PLAN
A6.1 MECHANICAL PLAN
A6.2 FIRST FLOOR FINISHES
A6.3 SECOND FLOOR FINISHES
A6.4 LOFT FLOOR FINISHES
A6.5 ARCHITECTURAL DETAILS
A6.6

ZOPHI UNITS

1055 ZOPHI ST
NASHVILLE, TN 37216

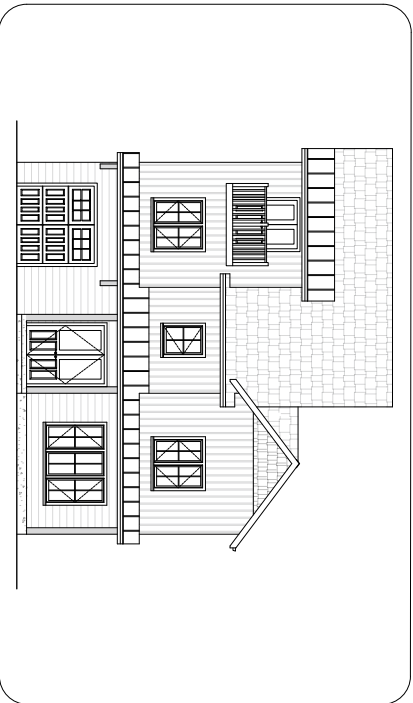

ABBREVIATIONS

A.C.	ABOVE COUNTER	C.N.C.	CONCRETE	E.A.	EACH	G.V.P.	GYPSUM	(N.)	NEW	R.D.	ROOF DRAIN	S.S.	STAINLESS STEEL
ALUM.	ALUMINUM	C.N.T.R.	COUNTER	E.P.	ELEVATION	H.R.	HANDICAPPED	N.I.C.	NOT IN CONTRACT	REF.	REFRIGERATOR	ST	STRUCTURAL
APPROX.	APPROXIMATE	C.W.	COLD WATER	F.D.	FLOOR DRAIN	H.W.	HEADER	N.T.S.	NOT TO SCALE	REIN.	REINFORCED	ST	TEMPERED GLASS
ARCH.	ARCHITECTURAL	D.B.A.O.	DRAWING BOARD APPROVED	F.F.	FLOOR FINISH	H.W.	HOT WATER	O.C.	ON CENTER	REIN.	REINFORCED	TEMP.	TEMPERED GLASS
B.D.M.	BEDROOM	D.I.A.	DIMENSION	F.F.	FINISHED FLOOR	H.W.	HOT WATER	P.L.	PROPERTY LINE	S.G.D.	SLIDING GLASS DOOR	T.O.F.	TOP OF FLOOR
BLKG.	BLOCKING	D.I.S.P.	DISPENSER	F.L.	FLASHING	I.D.	INSULATION	P.T.	PRESSURE TREATED	SHWR.	SHOWER	TYP.	TYPICAL
B.M.	BEDROOM	D.N.	DOWN	F.L.	FLOOR	I.D.	INSULATION	R.B.	REINFORCED	SHWR.	SHOWER	U.C.	UNDER COUNTER
B.A.G.	BATHING	D.N.	DOWN	F.L.	FLOOR	I.D.	INSULATION	R.B.	REINFORCED	SHWR.	SHOWER	U.C.	UNDER COUNTER
C.L.	CENTER LINE	D.W.	DISHWASHER	F.R.	FREE RATED	K.I.	KITCHEN	R.A.V.	RETURN AIR VENT	SPEC.	SPECIFICATION	U.S.	UNDER SIDE
C.G.	CLOSET	E.R.	EXISTING	G.C.	GENERAL CONTRACTOR	M.N.	MINIMUM	R.A.V.	RETURN AIR VENT	SPEC.	SPECIFICATION	U.S.	UNDER SIDE
C.I.S.T.	CLOSET	E.R.	EXISTING	G.C.	GENERAL CONTRACTOR	M.N.	MINIMUM	R.A.V.	RETURN AIR VENT	SPEC.	SPECIFICATION	U.S.	UNDER SIDE

draft.

ZOPHI UNITS

1055 ZOPHI ST
NASHVILLE, TN 37216


DRAWN BY: CM

DATE: 09/30/2025

SCALE:


STAMP

SHEET
COVER
PAGE
A0.0

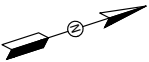

SITE PLAN

SCALE: 3/32" = 1'-0"

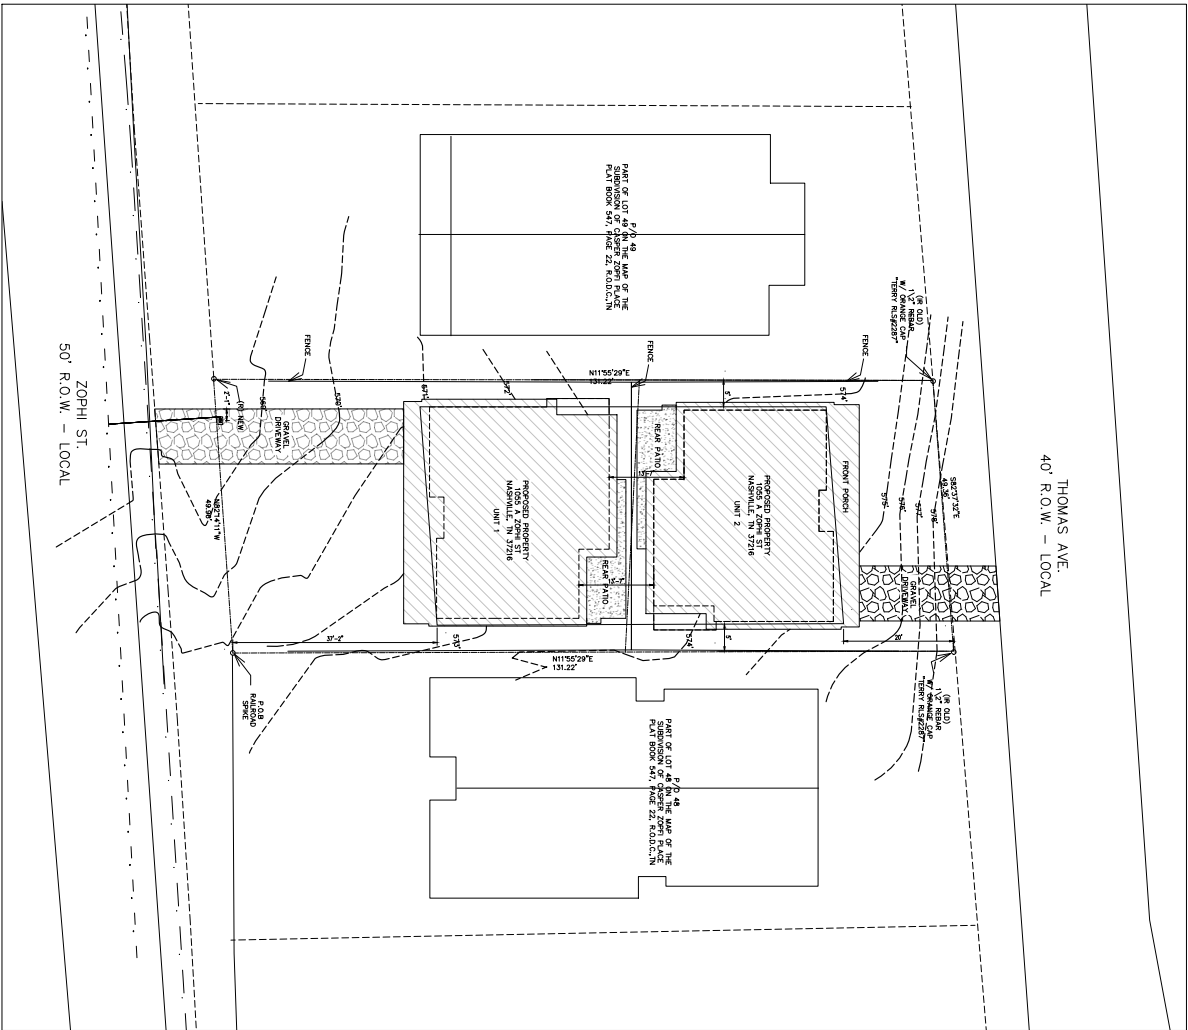

NOTE: ALL LOCATIONS AND MEASUREMENTS TO BE VERIFIED BY CONTRACTOR ON SITE PRIOR TO CONSTRUCTION.

draft.

THIS PLAN IS A PRELIMINARY DESIGN AND IS NOT TO BE USED FOR CONSTRUCTION. IT IS THE RESPONSIBILITY OF THE CLIENT TO OBTAIN ALL NECESSARY PERMITS AND TO VERIFY ALL MEASUREMENTS AND LOCATIONS ON SITE PRIOR TO CONSTRUCTION. THE CLIENT SHALL BE RESPONSIBLE FOR OBTAINING ALL NECESSARY PERMITS AND FOR VERIFYING ALL MEASUREMENTS AND LOCATIONS ON SITE PRIOR TO CONSTRUCTION. THE CLIENT SHALL BE RESPONSIBLE FOR OBTAINING ALL NECESSARY PERMITS AND FOR VERIFYING ALL MEASUREMENTS AND LOCATIONS ON SITE PRIOR TO CONSTRUCTION.

ZOPHI UNITS
1055 ZOPHI ST
NASHVILLE, TN 37216

DRAWN BY: CM

DATE: 08/19/2025

SCALE: 3/32" = 1'-0"


STAMP

SHEET

A1.0

SITE PLAN

1,020 SQ. FT. SCALE: 3/8" = 1'-0"

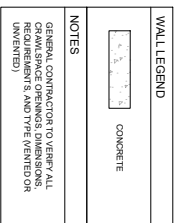[illegible]

DRAWN BY: CM

DATE: 09/19/2025


SCALE: 3/8" = 1'-0"

STAMP

SHEET

A2.0

CRAWLSPACE FLOOR PLAN

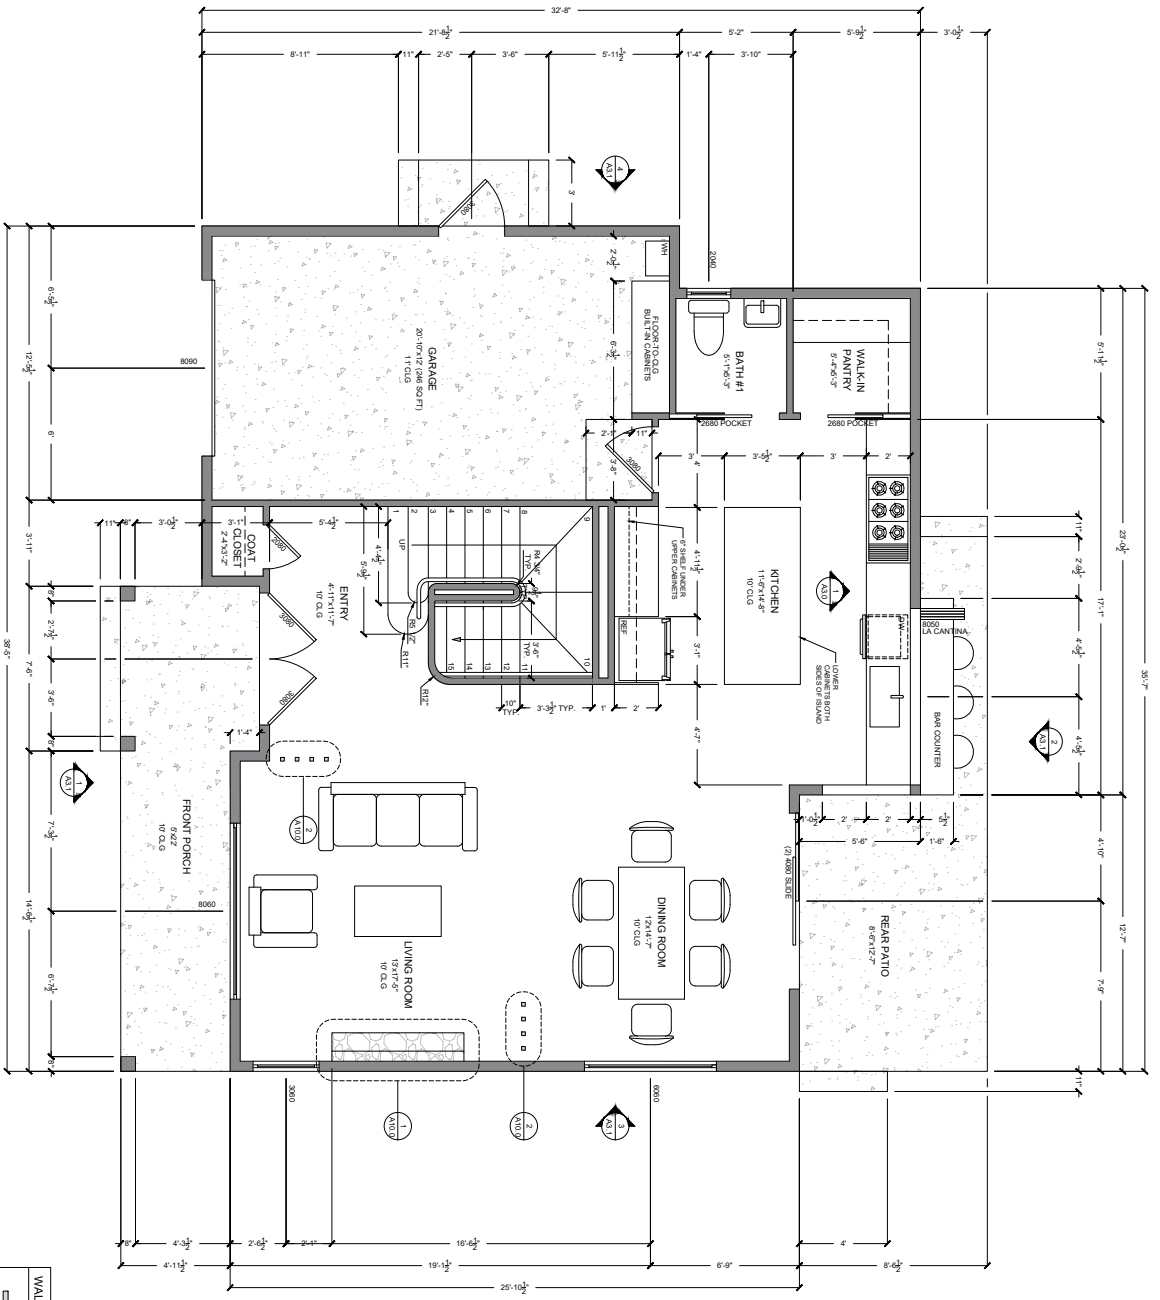

FIRST FLOOR PLAN
SCALE: 3/8" = 1'-0"

WALL LEGEND

	INTERIOR WALL
	- 4" FOR NON PLUMBING WALLS
	- 6" FOR PLUMBING WALLS
	- 8" THICKNESS
	CONCRETE


ZOPHI UNITS
1055 ZOPHI ST
NASHVILLE, TN 37216

draft.

A2.2
FIRST FLOOR
PLAN

SHEET
DRAWN BY: CM
DATE: 08/30/2025
SCALE: 3/8" = 1'-0"
STAMP

SCALE: 3/8" = 1'-0"

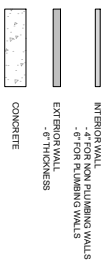

SECOND
FLOOR PLAN

NASHVILLE, TN 37216


SCALE: 3/8" = 1'-0"

STAMP

draft.

[illegible]

LOFT FLOOR PLAN
398 SQ FT
SCALE: 3/8" = 1'-0"

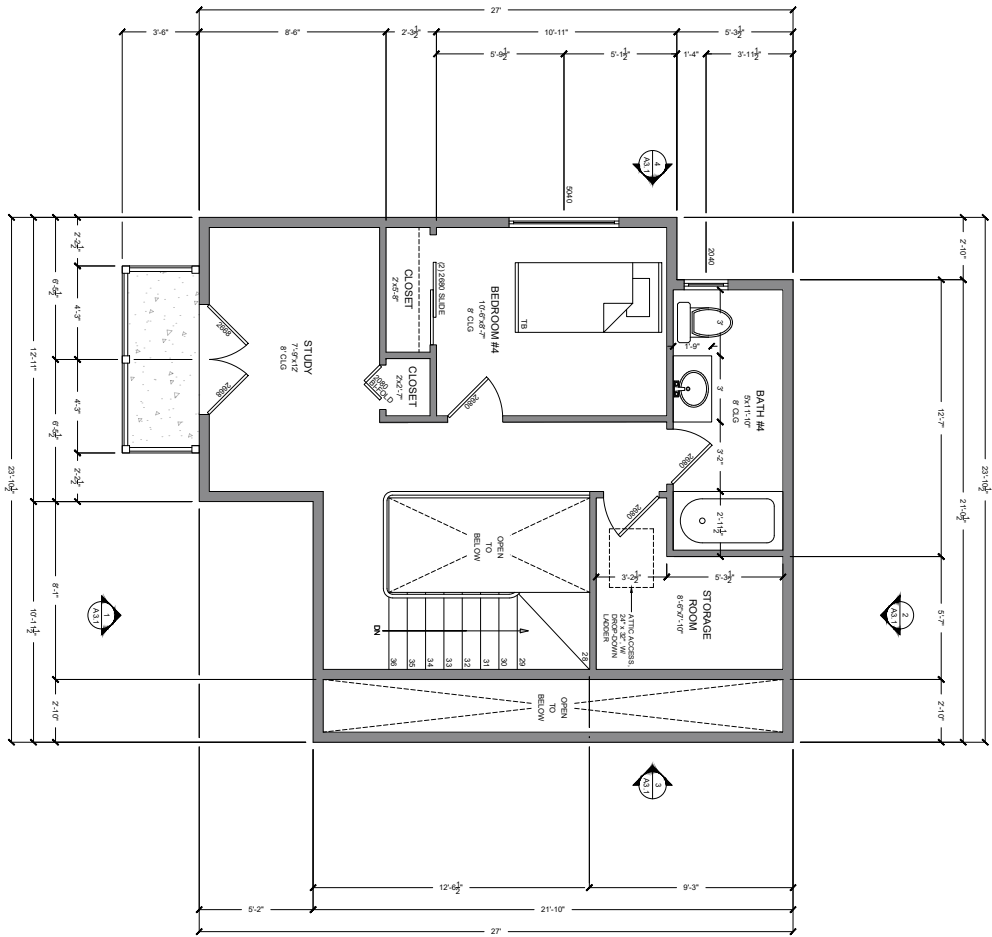

WALL LEGEND

	INTERIOR WALL
	EXTERIOR WALL
	CONCRETE


ZOPHI UNITS
1055 ZOPHI ST
NASHVILLE, TN 37216

draft.

THIS PLAN IS A PRELIMINARY DESIGN AND IS NOT TO BE USED FOR CONSTRUCTION. IT IS THE PROPERTY OF ZOPHI UNITS AND IS NOT TO BE REPRODUCED OR TRANSMITTED IN ANY FORM OR BY ANY MEANS, ELECTRONIC OR MECHANICAL, INCLUDING PHOTOCOPYING, RECORDING, OR BY ANY INFORMATION STORAGE AND RETRIEVAL SYSTEM. ANY VIOLATION OF THIS NOTICE IS A VIOLATION OF THE COPYRIGHT ACT OF 1976 AND WILL BE PROSECUTED TO THE FULL EXTENT OF THE LAW.

DRAWN BY: CM
DATE: 08/30/2025
SCALE: 3/8" = 1'-0"
STAMP

A2.4
LOFT FLOOR
PLAN

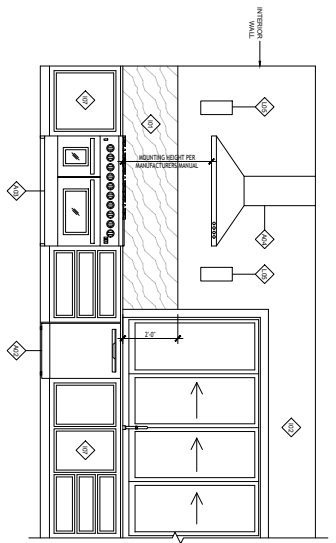

1 INTERIOR ELEVATION @ KITCHEN STOVE

draft.

DOES IT NOT BEING A LICENSED ARCHITECTURAL OR ENGINEERING FIRM, ASSIGNED SUBJECTS OF THE STUDY, BE AT A DISADVANTAGE IN THAT THE RESEARCHERS ARE NOT ABLE TO DRAW ON THEIR OWN KNOWLEDGE AND CONJECTURES TO COMPLEMENT THE DATA? SHOULD THEY BE REQUIRED TO COMPLEMENT THEIR CONCLUSIONS BY THE USE OF REASONABLE, OR THE CONJECTURES OF COMPELLED, THE DECISION TO NOT DRAW AND JUDICIAL CONNECTION IS REASONABLE FOR VARIOUS REASONS? ALL RESEARCHERS IN THE FIELD ARE PROHIBITED FROM DRAWING CONCLUSIONS OR STATING REASONABLE IN A LOCAL CODE.

ZOPHI UNITS
1055 ZOPHI ST
NASHVILLE, TN 37216

DRAWN BY: CM

DATE: 09/24/2025

SCALE: 3/4" = 1'-0"

STAMP


SHEET

A3.0

INTERIOR ELEVATIONS

ROOF PLAN

SCALE: 3/8" = 1'-0"

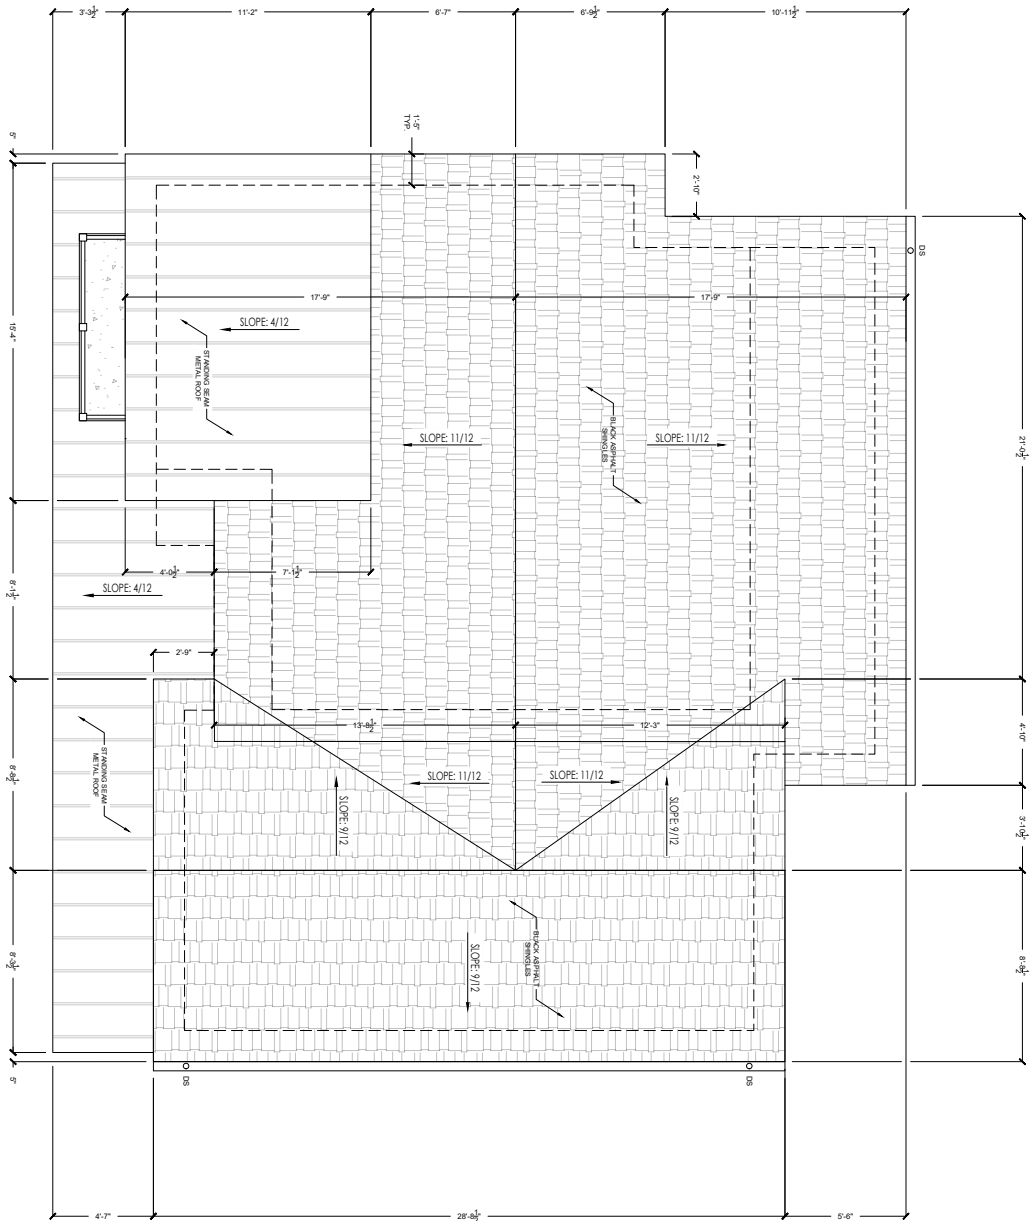

draft.

THIS IS A DRAFT OF A PRELIMINARY DESIGN. IT IS NOT TO BE USED FOR CONSTRUCTION. ANY CHANGES OR MODIFICATIONS TO THE DESIGN MUST BE APPROVED BY THE DESIGNER. THE DESIGNER ASSUMES NO LIABILITY FOR ANY ERRORS OR OMISSIONS IN THIS DESIGN. THE DESIGN IS BASED ON THE INFORMATION PROVIDED BY THE CLIENT. THE CLIENT ASSUMES RESPONSIBILITY FOR THE ACCURACY AND COMPLETENESS OF THE INFORMATION PROVIDED. THE DESIGN IS SUBJECT TO CHANGE WITHOUT NOTICE. THE DESIGN IS NOT TO BE USED FOR ANY OTHER PURPOSES WITHOUT THE WRITTEN CONSENT OF THE DESIGNER.

ZOPHI UNITS

1055 ZOPHI ST
NASHVILLE, TN 37216

DRAWN BY: CM

DATE: 08/28/2025

SCALE: 3/8" = 1'-0"

STAMP

SHEET

A5.0

ROOF PLAN

GENERAL NOTE

ALL CEILINGS SHALL BE PAINTED TO MATCH THE WALL COLOR OF THE SAME ROOM UNLESS OTHERWISE INDICATED ON THE DRAWINGS OR FINISH SCHEDULE.

EXTERIOR FINISHES SCHEDULE

#	ITEM DESCRIPTION	PRICE
607	BOARD AND BATTEN, OFF WHITE (UNIT 1)	N/A
608	BOARD AND BATTEN, FLAGSHIP BROWN (UNIT 2)	N/A

FLOOR FINISHES SCHEDULE

#	ITEM DESCRIPTION	PRICE
609	CONCRETE STAIN, BEHR PREMIUM, WHITE MODEL #. 80001	\$36.98/GAL
610	ENGINEERED HARDWOOD, LIFEROOF, SHEMAMDOAH OAK, MODEL #.: VYMHDSHED0AK7X75	\$4.63/SQ. FT
611	TILE, EDWARD MARTIN, LEONA, 12"X12", POLISHED, MARFIL AND AMAN BRONZE, SKU #.: 11881	\$11.49/SQ. FT
612	WOOD STAIRS, OAK, STAINED TO MATCH FLOORING	N/A

INTERIOR FINISHES SCHEDULE


#	ITEM DESCRIPTION	PRICE
613	COUNTERTOP, EONYX STONE, MARBLE, DIANO REALE BEIGE	N/A
614	PAINT, VALSPAR, QUALE EGG, EGGSHELL FINISH COLOR CHIP: 7002-12	\$48.98/GAL
615	PAINT, VALSPAR, ULTRA WHITE, EGGSHELL FINISH COLOR CHIP: 7006-24	\$46.98/GAL
616	PAINT, VALSPAR, WINDMILL, EGGSHELL FINISH COLOR CHIP: 8005-10C	\$52.98/GAL
617	STONE VENEER, MAROCK, WOODLAND/SHAWVILLE FIELD STONE, TRADITIONAL, MORTARED	\$68.00/BOX
618	CUSTOM IRON RAILING W/ WOOD HANDRAIL (COLOR TO MATCH STAIR)	N/A
619	LOWER CABINETS, CUSTOM BUILT, OAK, MEDIUM-DARK BROWN, SLIM AND HARDWARE-FREE	N/A
620	UPPER WOOD CABINETS, CUSTOM BUILT, OAK, MEDIUM-DARK BROWN, SLIM AND HARDWARE-FREE	N/A

APPLIANCES SCHEDULE

#	ITEM DESCRIPTION	PRICE
621	KITCHEN SINK, KOHLER, UNDERMOUNT MODEL #. K-80084-1PC-1A	\$288.28/EA
622	DISHWASHER, FRIGIDAIRE, STAINLESS STEEL, POCKET HANDLE, MODEL #.: GDP4515AF	\$625.00/EA
623	GAS RANGE W/ DOUBLE OVENS, FORNO, GALIANO MODEL #.: FFGSG924-48	\$4,599.00/EA
624	RANGE HOOD, BRANO MODEL #.: LAM05-48	\$742.18/EA
625	REFRIGERATOR, FRIGIDAIRE, FRENCH DOORS MODEL #.: FRFN28134F	\$1,448.00/EA
626	BATHROOM SINK, AMAZON, VAPORINT, WHITE, 20" X 17" ASIN #.: B0CHB8RT143	\$119.99/EA
627	TOILET, SWISS MADISON, SUBLIME II MODEL #.: SM-11257	\$239.00/EA
628	ELECTRIC FIREPLACE, AMAZON, RICHFLAME, EDWARD 33" X 28", CONCRETE INTERIOR, ASIN #.: B0B1DHZXJR	\$359.99/EA

SPECIALTY LIGHTING SCHEDULE

#	ITEM DESCRIPTION	PRICE
629	CHANDELIER, POTTERY BARN, WINDHAM, 42" SKU #.: SKU: 9282300	\$699.00/EA
630	WALL SCONCE, POTTERY BARN, WINDHAM, ALABASTER SKU #.: 3975705	\$299.00/EA
631	CHANDELIER, POTTERY BARN, EMORY, 50" SKU #.: N/A	\$499.00/EA
632	PENDANT LIGHT, POTTERY BARN, CAMRYN, 49" SKU #.: 5065280	\$799.00/EA
633	WALL SCONCE, POTTERY BARN, AMALIA, ALABASTER SKU #.: 6021228	\$349.00/EA
634	WALL SCONCE, POTTERY BARN, COOPER, BRONZE SKU #.: 121029	\$249.00/EA
635	WALL SCONCE, AMAZON, TARENTLIGHT, OIL-RUBBED BRONZE, 2-PAK, ASIN #.: B0F8B31B17	\$64.98/EA
636	CEILING LIGHT, POTTERY BARN, COOPER, BRONZE SKU #.: 1993325	\$299.00/EA

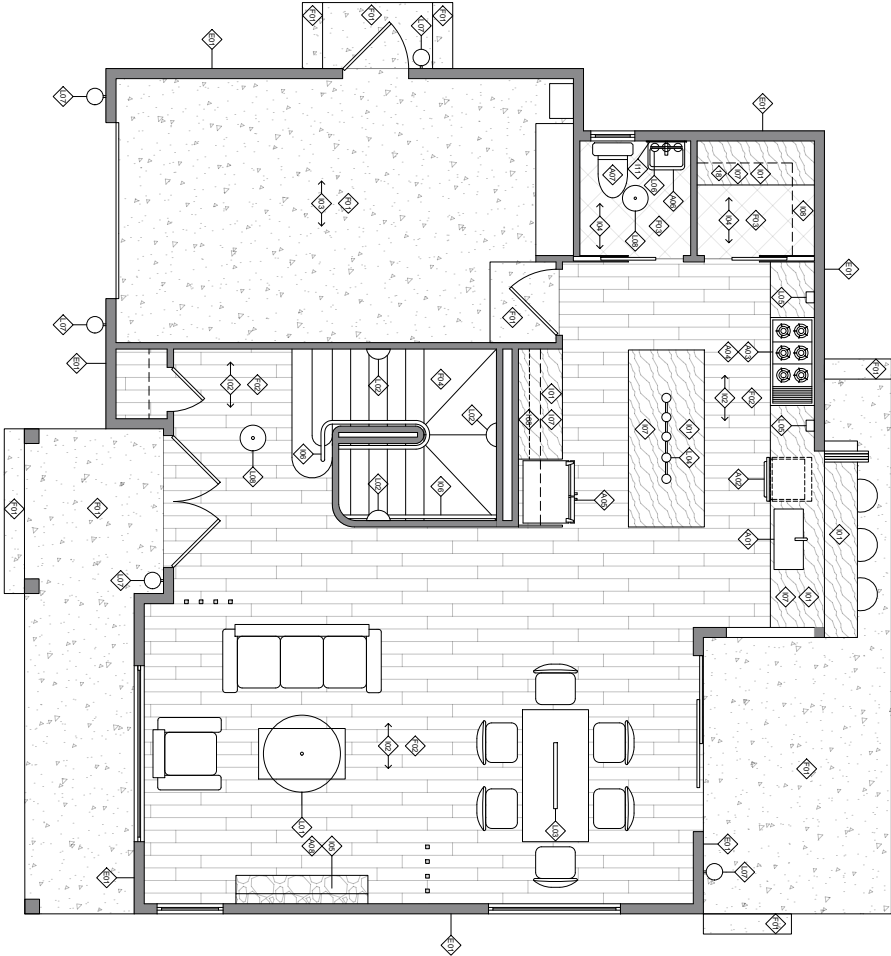

FIRST FLOOR FINISHES PLAN

SCALE: 3/8" = 1'-0"

draft.

ZOPHI UNITS

1055 ZOPHI ST
NASHVILLE, TN 37216

DRAWN BY: CM

DATE: 09/29/2025

SCALE: 3/8" = 1'-0"

STAMP

SHEET

A9.0

FIRST FLOOR
FINISHES

GENERAL NOTES

ALL CEILINGS SHALL BE PAINTED TO MATCH THE WALL COLOR OF THE SAME ROOM UNLESS OTHERWISE INDICATED ON THE DRAWINGS OR FINISH SCHEDULE.

EXTERIOR FINISHES SCHEDULE

#	ITEM DESCRIPTION	PRICE
607	BOARD AND BATTEN, OFF WHITE (UNIT 1)	N/A
608	BOARD AND BATTEN, FLAGSHIP BROWN (UNIT 2)	N/A

FLOOR FINISHES SCHEDULE

#	ITEM DESCRIPTION	PRICE
609	ENGINEERED HARDWOOD, LIFEPROOF, SHENANDOAH OAK, MODEL #. YTMHDSHEOAK7X75	\$4.63/SQ FT
610	TILE, EDWARD MARTIN, LEONA, 12"x12", POLISHED, MARFIL AND AMANI BRONZE, SKU #. 11881	\$11.49/SQ FT
611	WOOD STAIRS, OAK, STAINED TO MATCH FLOORING	N/A

INTERIOR FINISHES SCHEDULE


#	ITEM DESCRIPTION	PRICE
612	PAINT, VALSPAR, QUAL EGG, EGGSHELL FINISH COLOR CHIP- 7002-12	\$48.98/GAL
613	STONE VENEER, MAROCK, WOODLAND/SHAMSVILLE	\$68.00/BOX
614	FIELD STONE, TRADITIONAL MORTARED	N/A
615	CUSTOM IRON RAILING W/ WOOD HANDRAIL (COLOR TO MATCH STAIR)	N/A
616	TUB FAUCET SYSTEM, SIGNATURE HARDWARE, NAPIER, OIL-RUBBED BRONZE, MODEL #. 422778	\$702.45/EA
617	FAUCET AND HANDLES SIGNATURE HARDWARE, TRITON WALL-MOUNT, OIL RUBBED BRONZE, MODEL #. SH453245	\$366.45/EA
618	MIRROR, JESS & MAIN, KET	\$357.00/EA
619	SHOWER SYSTEM, FENNOGASA, POLARIS SKU #. FCH01005	\$309.99/EA
620	WALL TILE, EDWARD MARTIN, PALMER, 6" X 24", GLOSSY, SAND, SKU #. 11027	\$5.22/SQ FT
621	FLOOR TO CEILING CABINETS, CUSTOM BUILT, OAK MEDIUM-DARK BROWN, SLIM AND HARDWARE-FREE	N/A
622	COUNTERTOP, EONYX STONE, LIMESTONE, CREMA PEARL	N/A
623	VANITY BASE, ARIEL, CAMBRIDGE, 72", OAK SKU #. A072D-BC-WO-A	\$1,860.00/EA

APPLIANCES SCHEDULE

#	ITEM DESCRIPTION	PRICE
624	TOILET, SWISS MADISON, SUBLIME II MODEL #. SM-11257	\$239.00/EA
625	ELECTRIC FIREPLACE, AMAZON, RICHFLAME, EDWARD 33" X 26", CONCRETE INTERIOR, ASIN #. B08DHDZJXR	\$359.99/EA
626	TUB, SIGNATURE HARDWARE, SITKA, 60" X 36", RIGHT DRAIN, MODEL #. SHSKS9038RW/H	\$1,099.00/EA
627	TUB, SIGNATURE HARDWARE, DREAMLINE, NILE MODEL #. BTUL2654XC/D	\$1,069.99/EA
628	WASHER AND DRYER STACKABLE SET, SAMSUNG BESPOKE, MODEL #. WV53BB8700AV	\$2,798.00/EA

SPECIALTY LIGHTING SCHEDULE

#	ITEM DESCRIPTION	PRICE
629	WALL SCONCE, POTTERY BARN, WINDHAM, ALABASTER SKU #. 3975705	\$299.00/EA
630	CEILING LIGHT, POTTERY BARN, COOPER, BRONZE SKU #. 1993325	\$299.00/EA
631	WALL SCONCE, POTTERY BARN, FRANCES, ALABASTER, BRONZE, SKU #. 8145907	\$249.00/EA

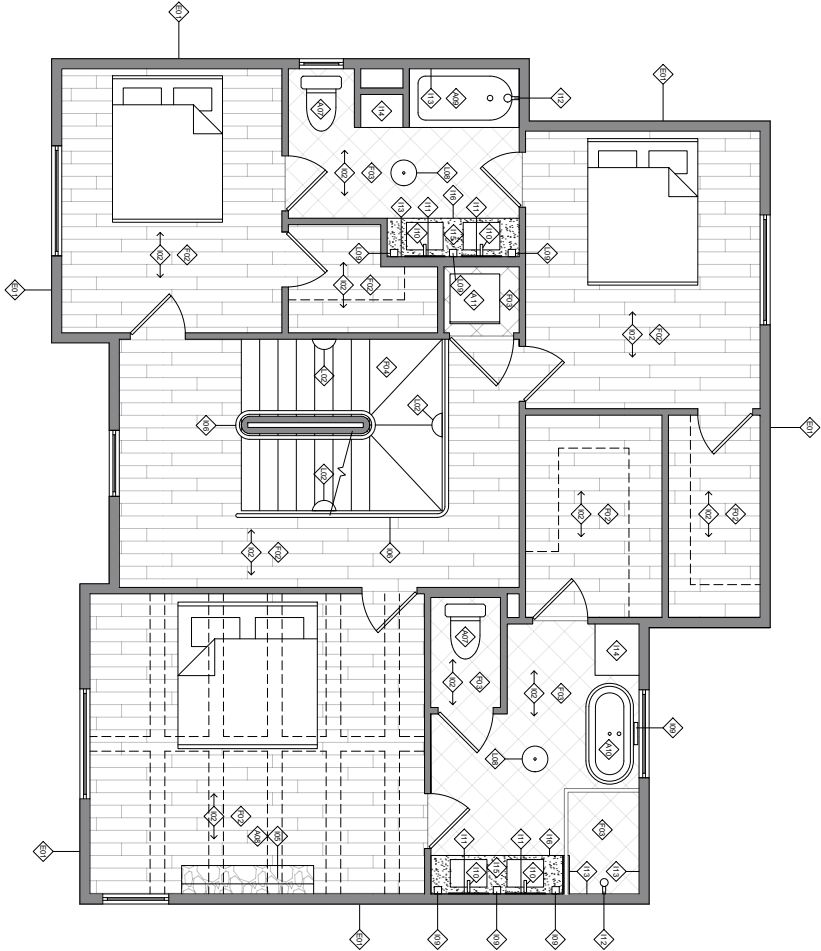

GENERAL NOTES

ALL CEILINGS SHALL BE PAINTED TO MATCH THE WALL COLOR OF THE SAME ROOM UNLESS OTHERWISE INDICATED ON THE DRAWINGS OR FINISH SCHEDULE.

EXTERIOR FINISHES SCHEDULE

#	ITEM DESCRIPTION	PRICE
60	BOARD AND BATTEN, OFF WHITE (UNIT 1)	N/A
60	BOARD AND BATTEN, FLAGSHIP BROWN (UNIT 2)	N/A

FLOOR FINISHES SCHEDULE

#	ITEM DESCRIPTION	PRICE
60	ENGINEERED HARDWOOD, LIFEPROOF, SHEMANOAH OAK, MODEL # VTYHDSHOAKTX75	\$4.63/SQ.FT
60	TILE, EDWARD MARTIN, LEONA, 12"X12", POLISHED, MARFIL AND AMANI BRONZE, SKU #: 11881	\$11.49/SQ.FT
60	WOOD STAIRS, OAK, STAINED TO MATCH FLOORING	N/A

INTERIOR FINISHES SCHEDULE


#	ITEM DESCRIPTION	PRICE
60	PAINT, VALSPAR, QUAIL EGG, EGGSHELL FINISH, COLOR CHIP, 7002-12	\$448.98/GAL
60	CUSTOM IRON RAILING W/ WOOD HANDRAIL (COLOR TO MATCH STAIR)	N/A
60	FAUCET AND HANDLES, SIGNATURE HARDWARE, TRITON WALL-MOUNT, OIL RUBBED BRONZE, MODEL # SH453245	\$366.45/EA
60	MIRROR, JOSSE & MAIN, KEIT, SKU #: W011049567	\$357.00/EA
60	SHOWER SYSTEM, FENNOGASA, POLARIS, SKU #: FCNO1005	\$309.99/EA
60	WALL TILE, EDWARD MARTIN, PALMER, 6" X 24", GLOSSY, SAND, SKU #: 11027	\$5.22/SQ.FT
60	VANITY, ARIEL, CAMBRIDGE, 37", OAK, SKU #: A037SLWCRCWOA	\$1,680.00/EA

APPLANCES SCHEDULE


#	ITEM DESCRIPTION	PRICE
60	TOILET, SWISS MADISON, SUBLIME II, MODEL #, SM-11297	\$239.00/EA
60	TUB, SIGNATURE HARDWARE, SITKA, 60" X 36", RIGHT DRAIN, MODEL #, SHKS6036RWVH	\$1,099.00/EA

SPECIALTY LIGHTING SCHEDULE


#	ITEM DESCRIPTION	PRICE
60	WALL SCONCE, POTTERY BARN, WINDHAM, ALABASTER, SKU #: 3973705	\$299.00/EA
60	WALL SCONCE, AMAZON, TARENTLIGHT, OIL-RUBBED BRONZE, 2-PACK, ASIN #: B0PB831B17	\$64.98/EA
60	CEILING LIGHT, POTTERY BARN, COOPER, BRONZE, SKU #: 1993325	\$299.00/EA
60	WALL SCONCE, POTTERY BARN, FRANCES, ALABASTER, BRONZE, SKU #: 8145907	\$249.00/EA
60	CEILING LIGHT, FLUSH MOUNT, POTTERY BARN, GEMMA, CRYSTAL, TIERED, SKU #: N/A	\$599.00/EA

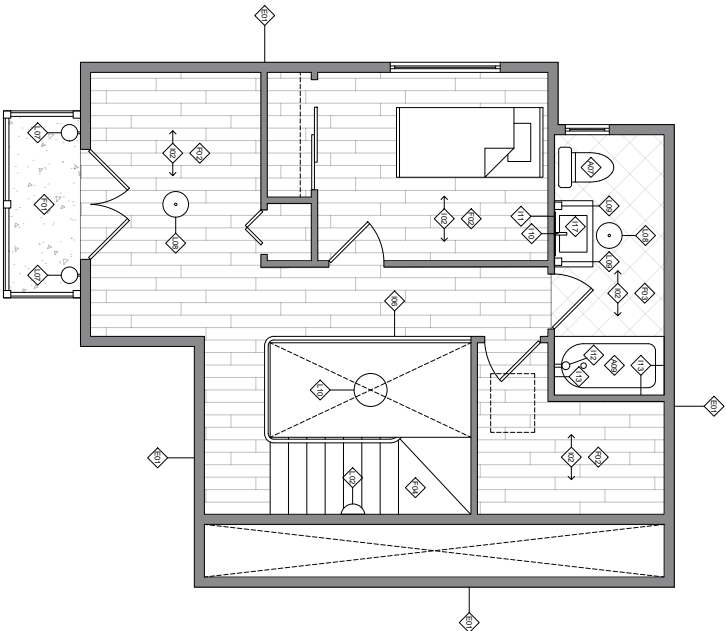

1 FIREPLACE DETAIL
SCALE: 3/4" = 1'-0"

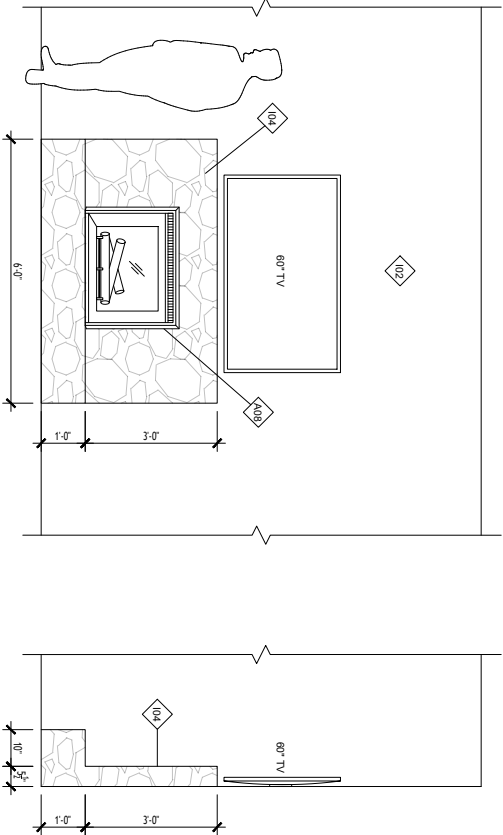

2 WOOD SLAT DETAIL @ WALL
SCALE: 3/4" = 1'-0"

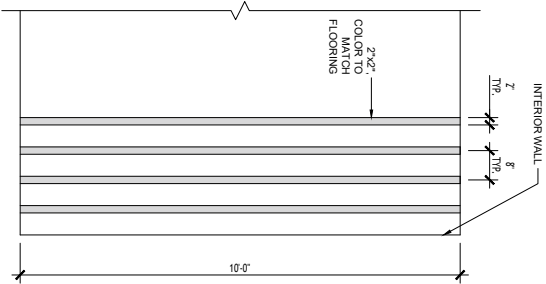

draft.

DRAFT ARCHITECTURE, PLLC
1055 ZOPHI STREET, SUITE 200
NASHVILLE, TN 37216
(615) 259-1234
WWW.DRAFTARCHITECTURE.COM

ZOPHI UNITS
1055 ZOPHI ST
NASHVILLE, TN 37216

DRAWN BY: CM

DATE: 08/24/2025

SCALE: 3/4" = 1'-0"

STAMP

SHEET

A10.0

ARCHITECTURAL
DETAILS